


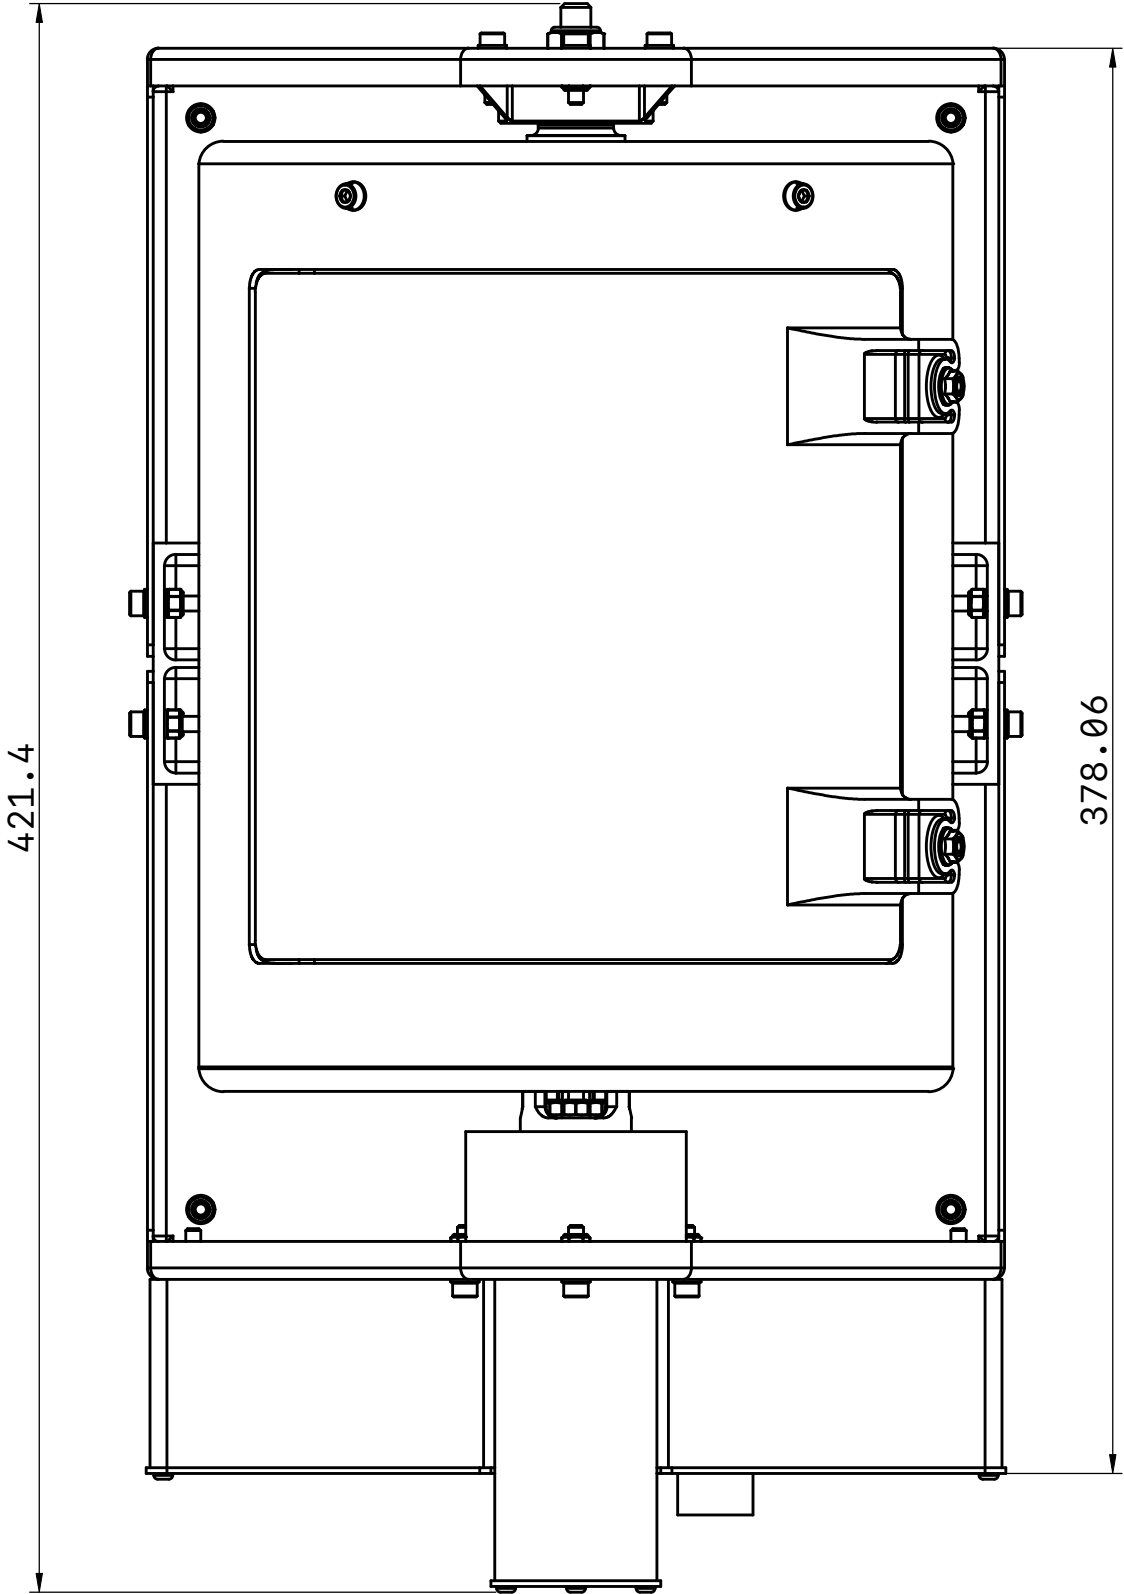


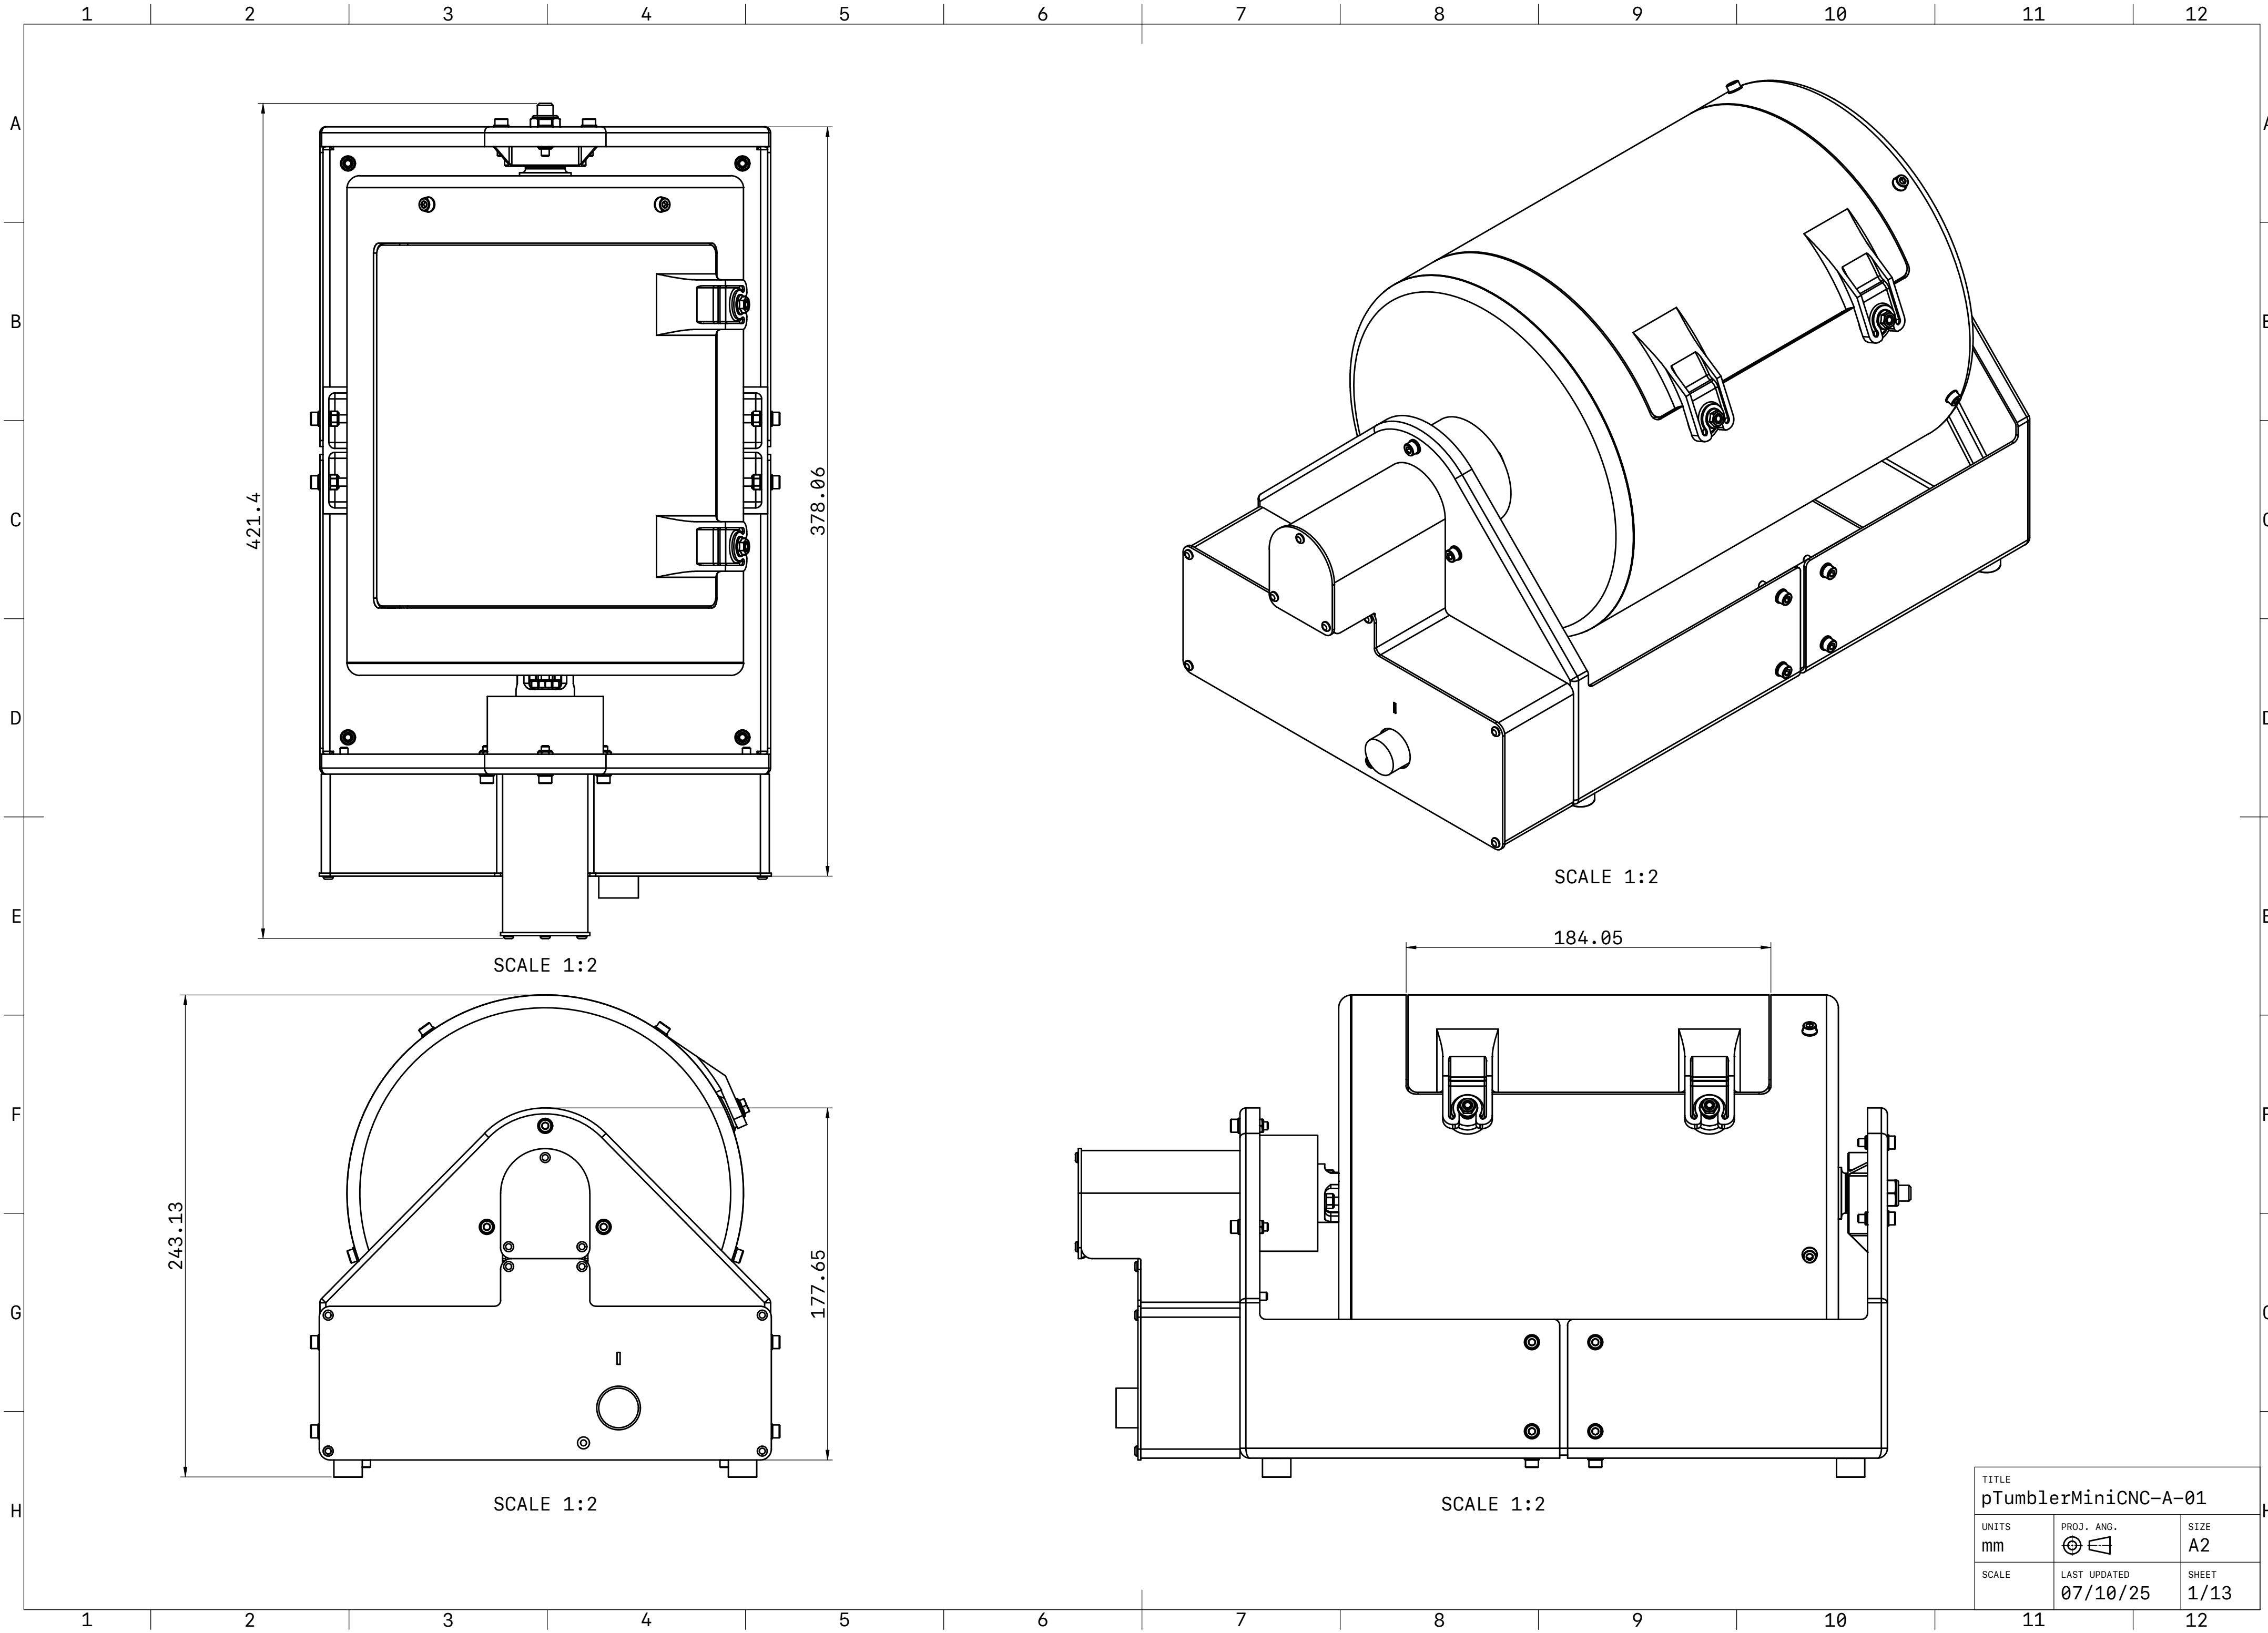


SCALE 1:2

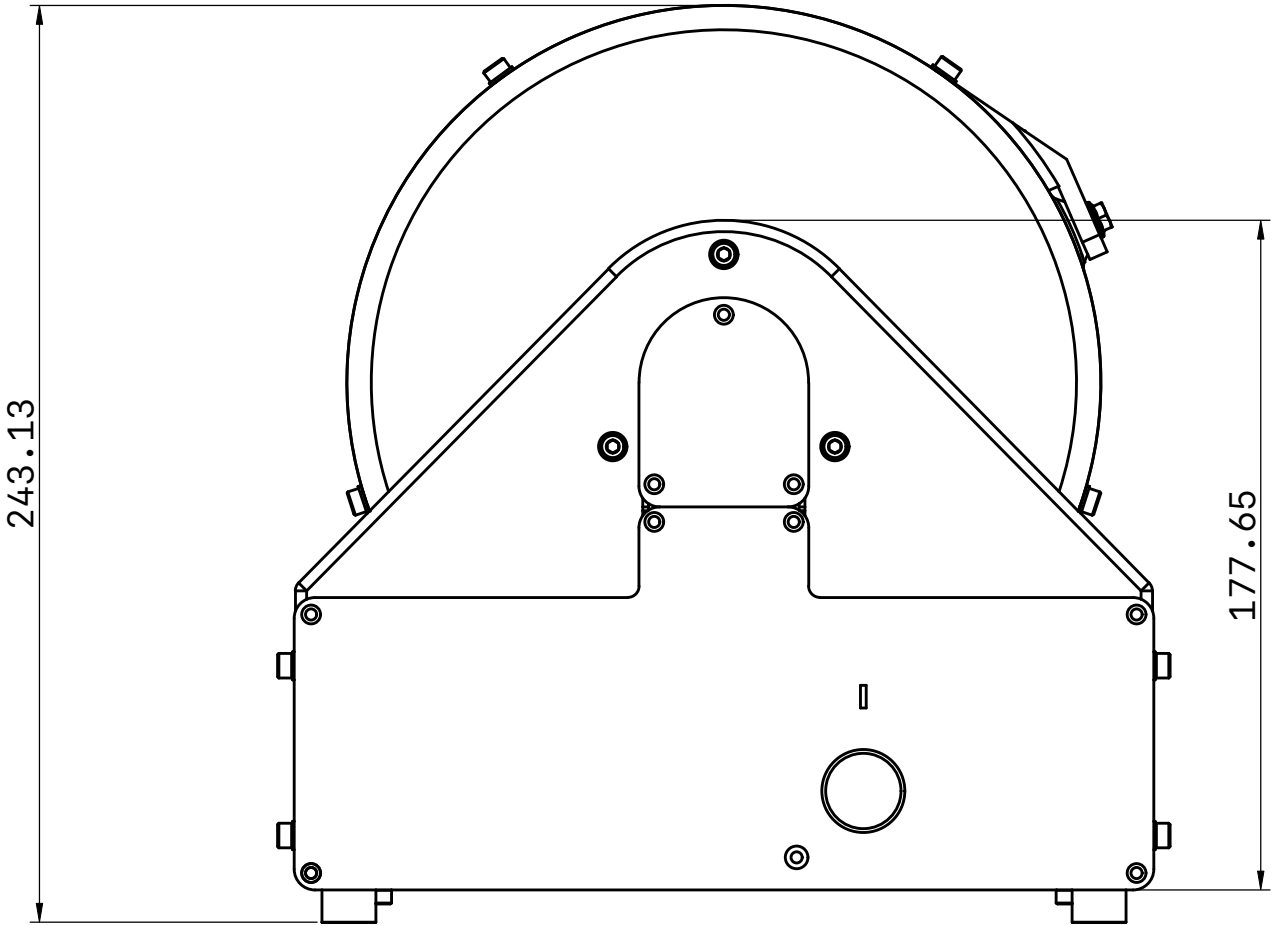

SCALE 1:2

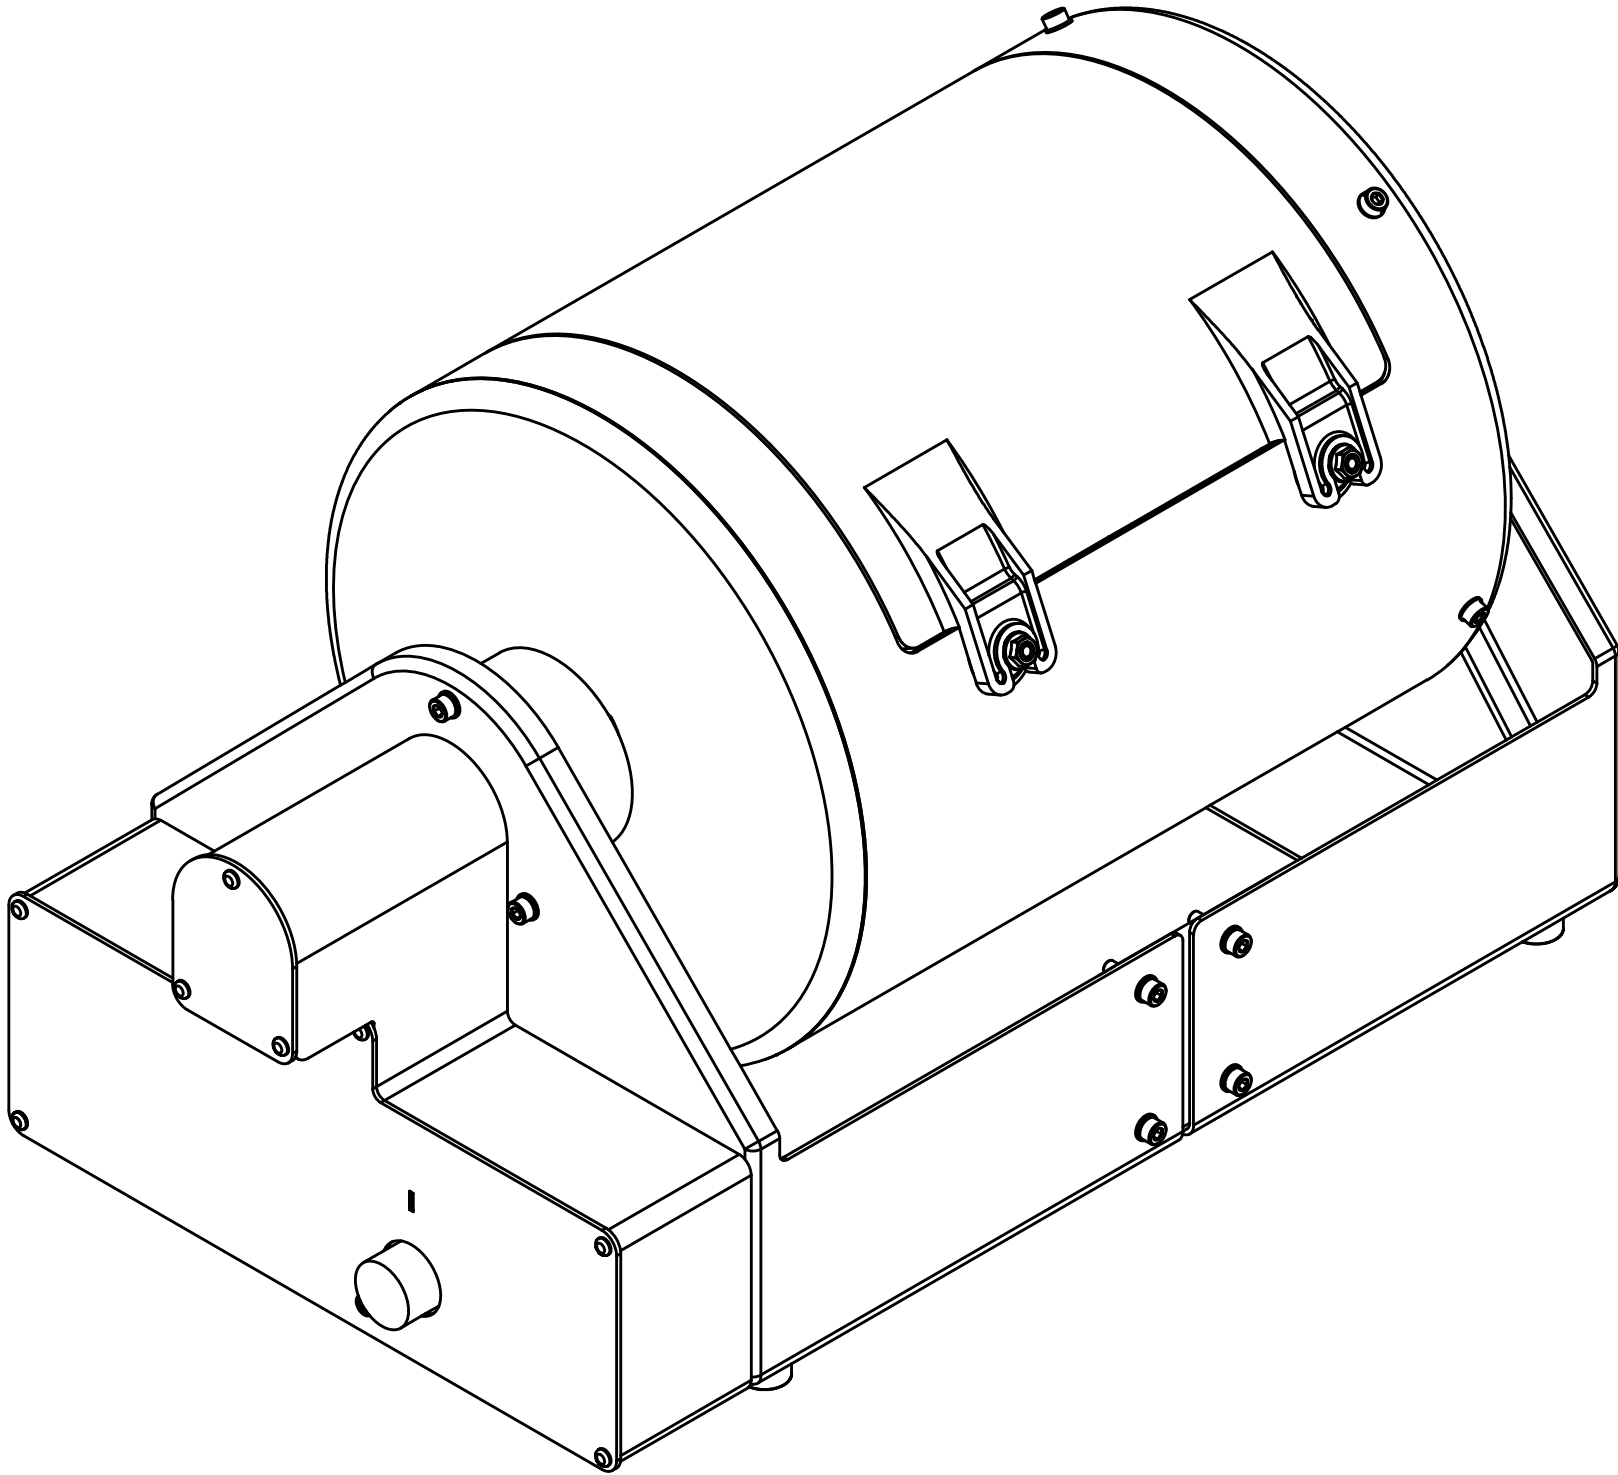


SCALE 1:2

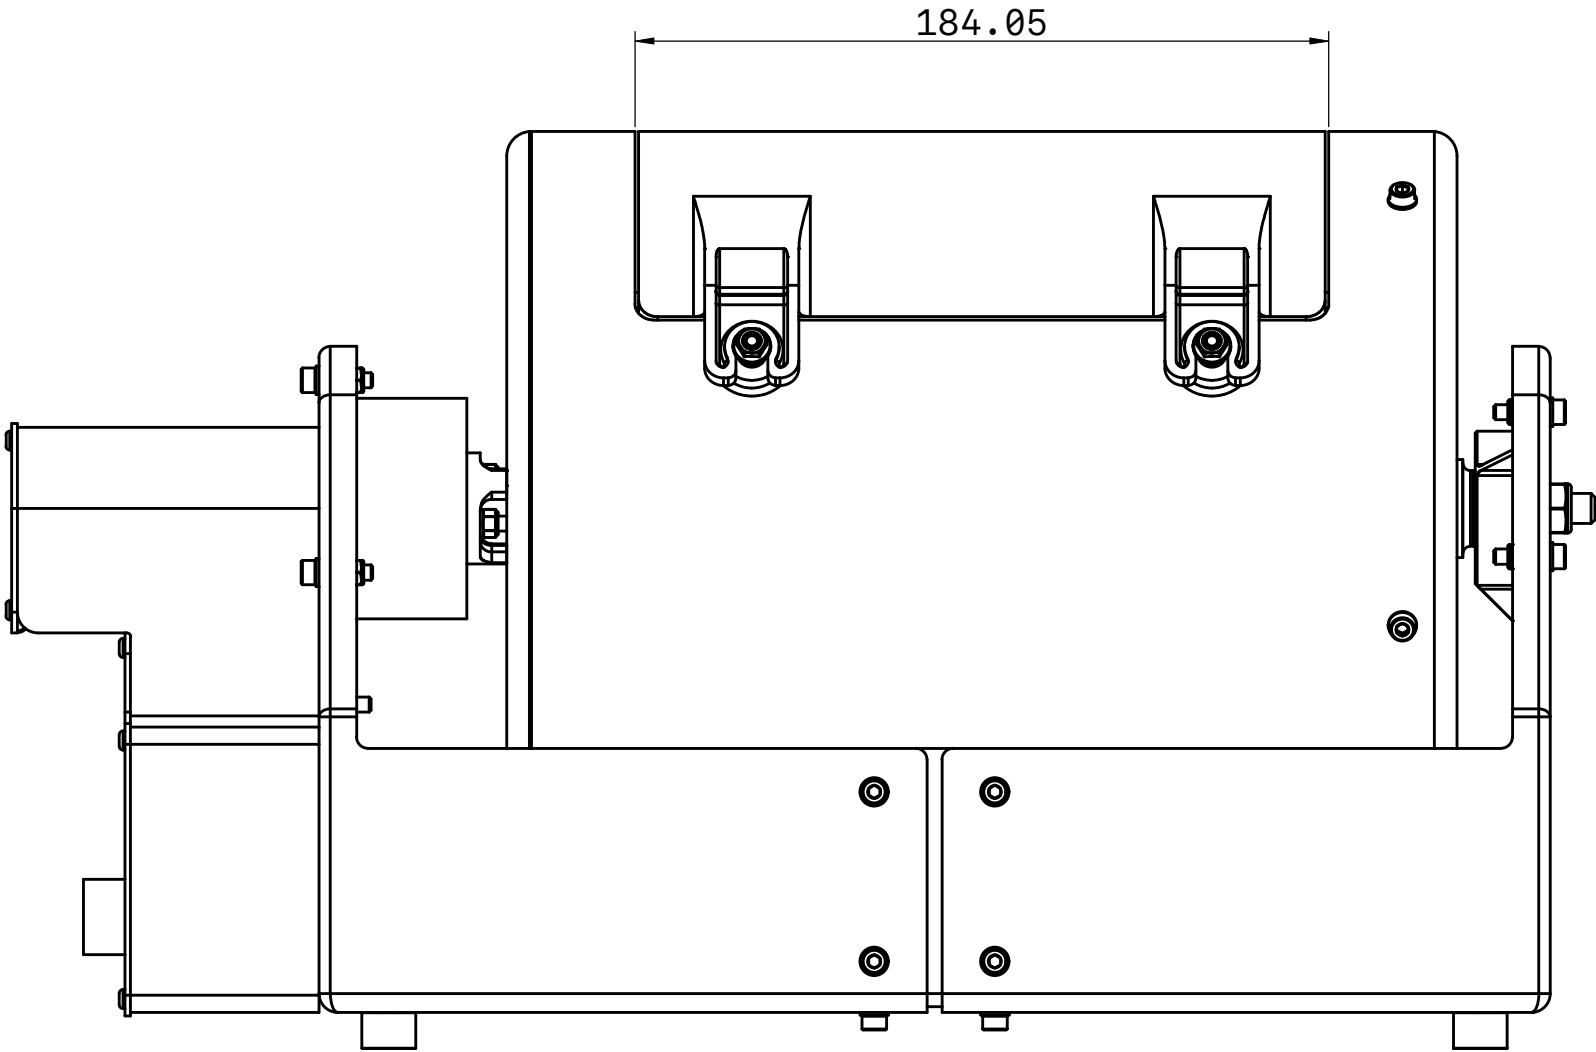


SCALE 1:2


TITLE pTumblerMiniCNC-A-01		
UNITS mm	PROJ. ANG. ⊕	SIZE A2
SCALE	LAST UPDATED 07/10/25	SHEET 1/13

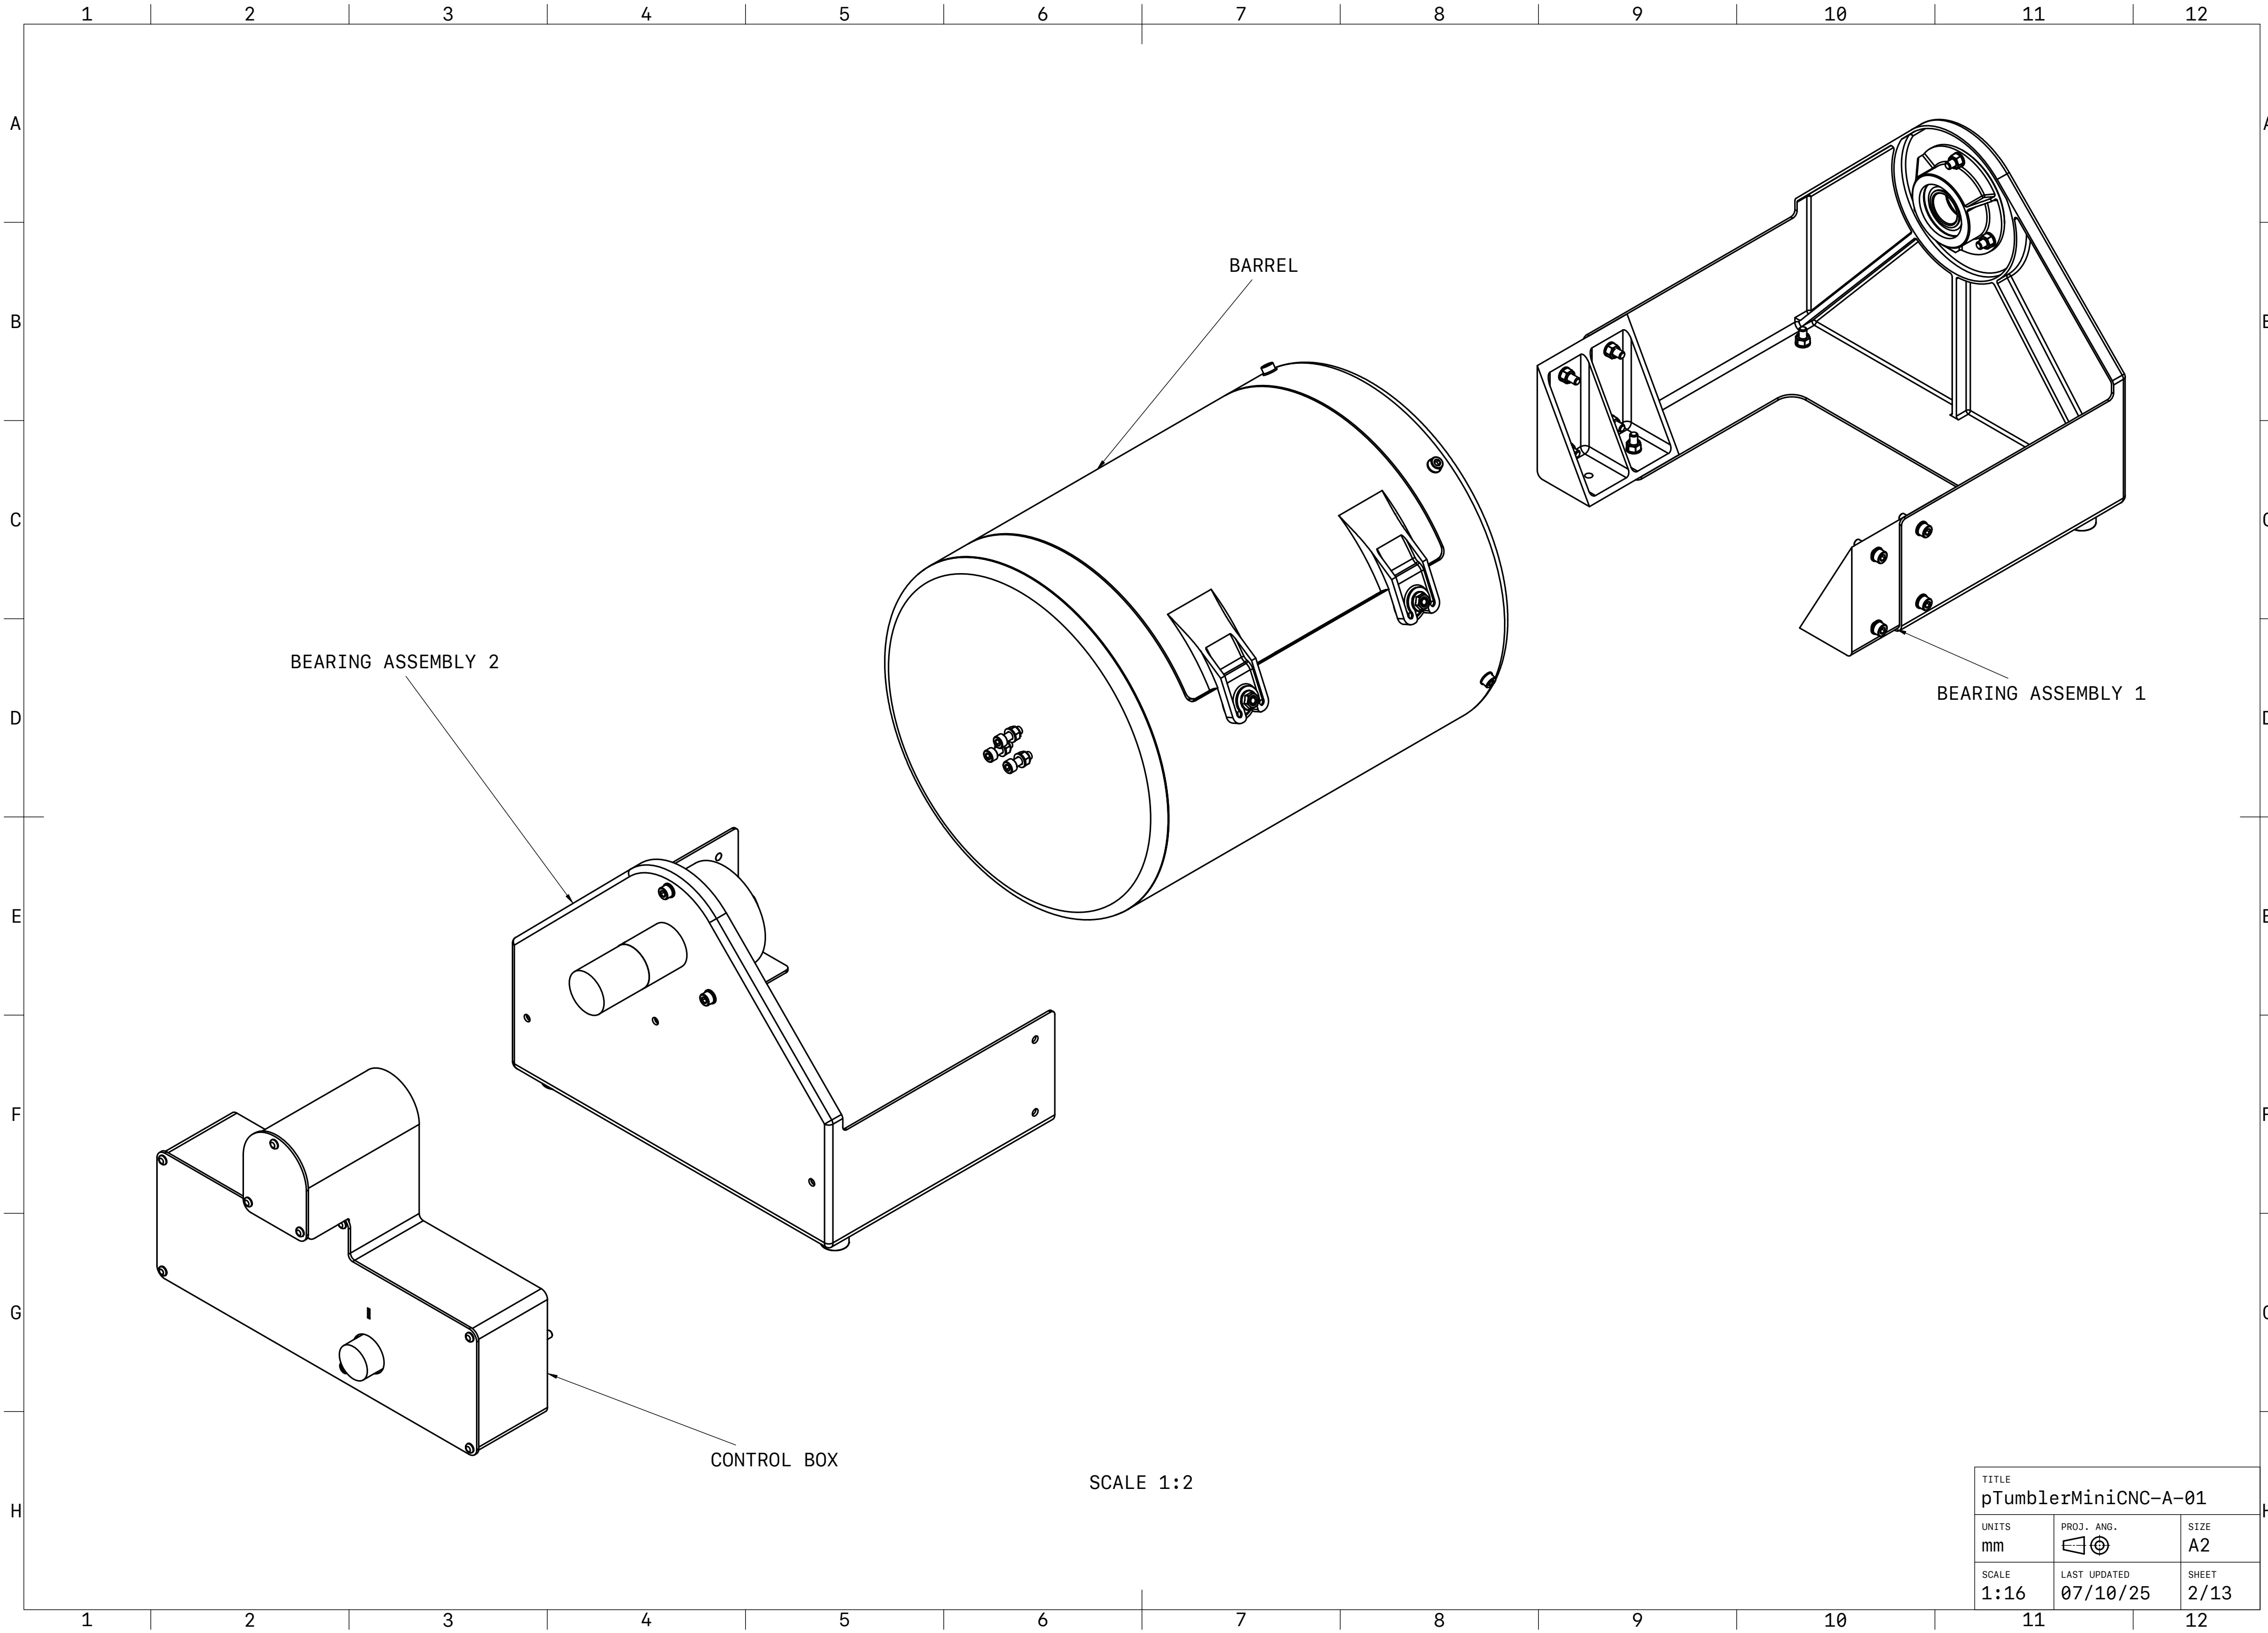



TITLE pTumblerMiniCNC-A-01		
UNITS mm	PROJ. ANG. 	SIZE A2
SCALE 1:16	LAST UPDATED 07/10/25	SHEET 2/13

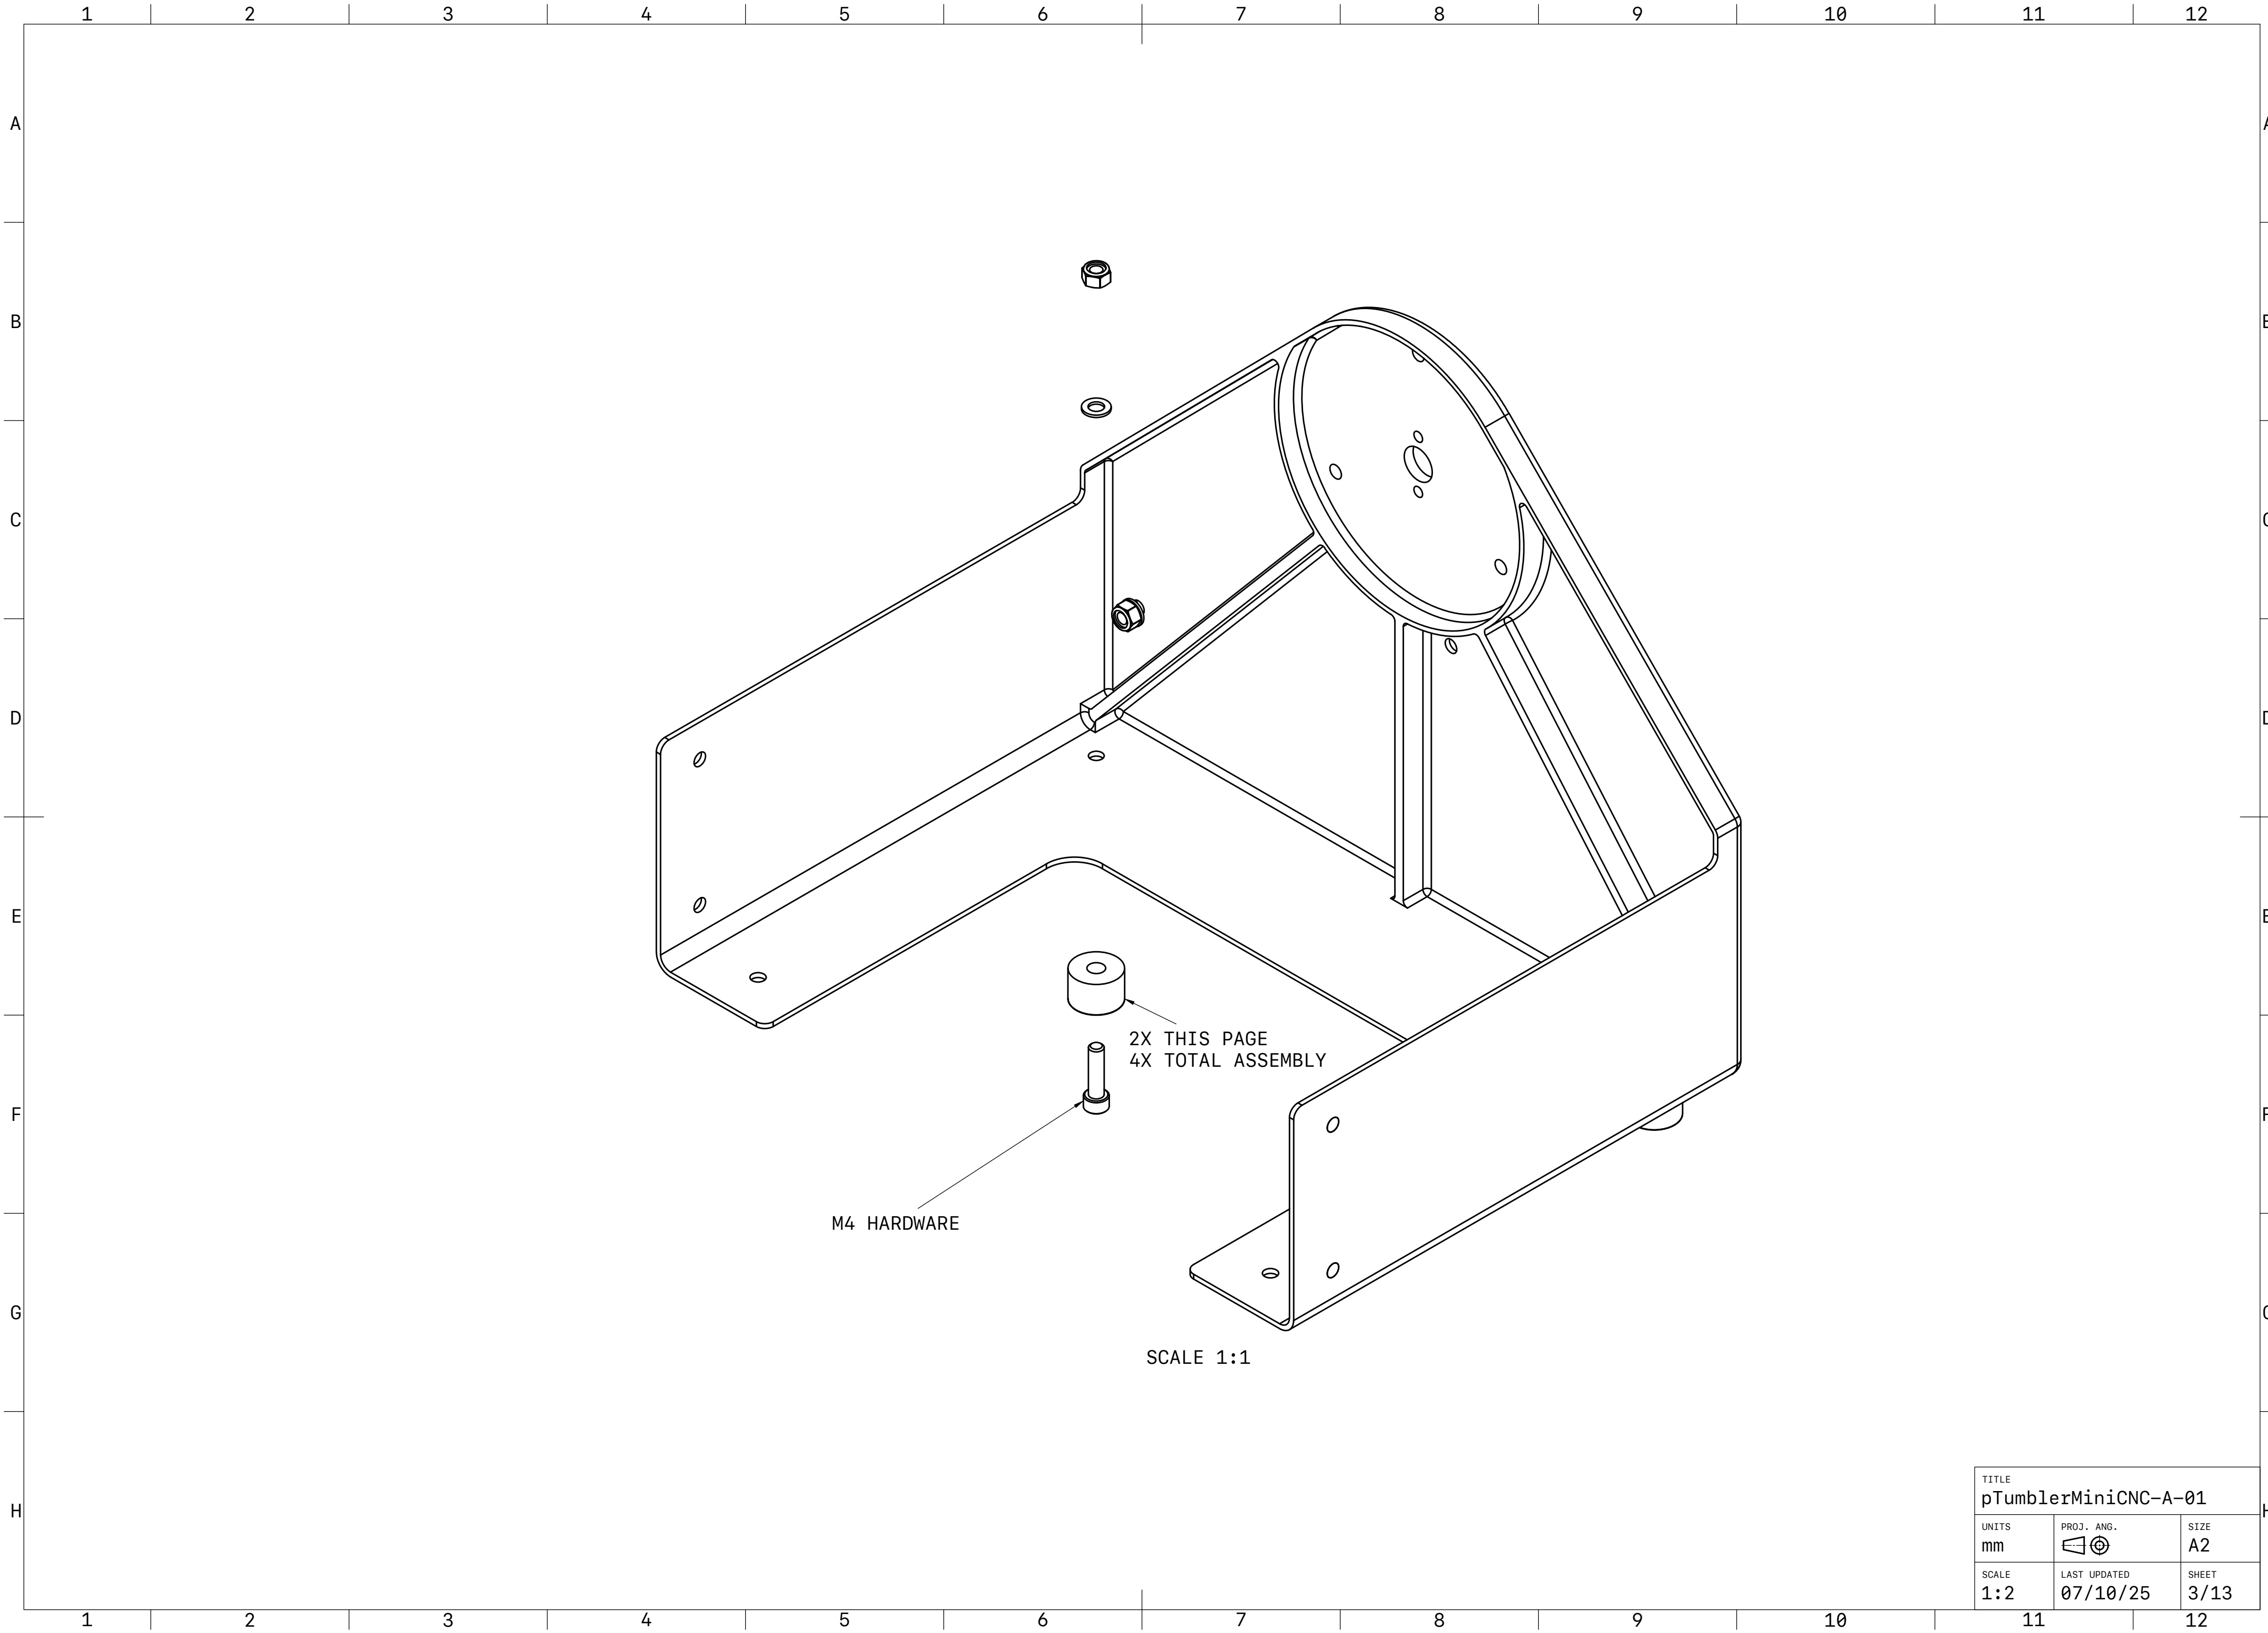

TITLE pTumblerMiniCNC-A-01		
UNITS mm	PROJ. ANG. 	SIZE A2
SCALE 1:2	LAST UPDATED 07/10/25	SHEET 3/13

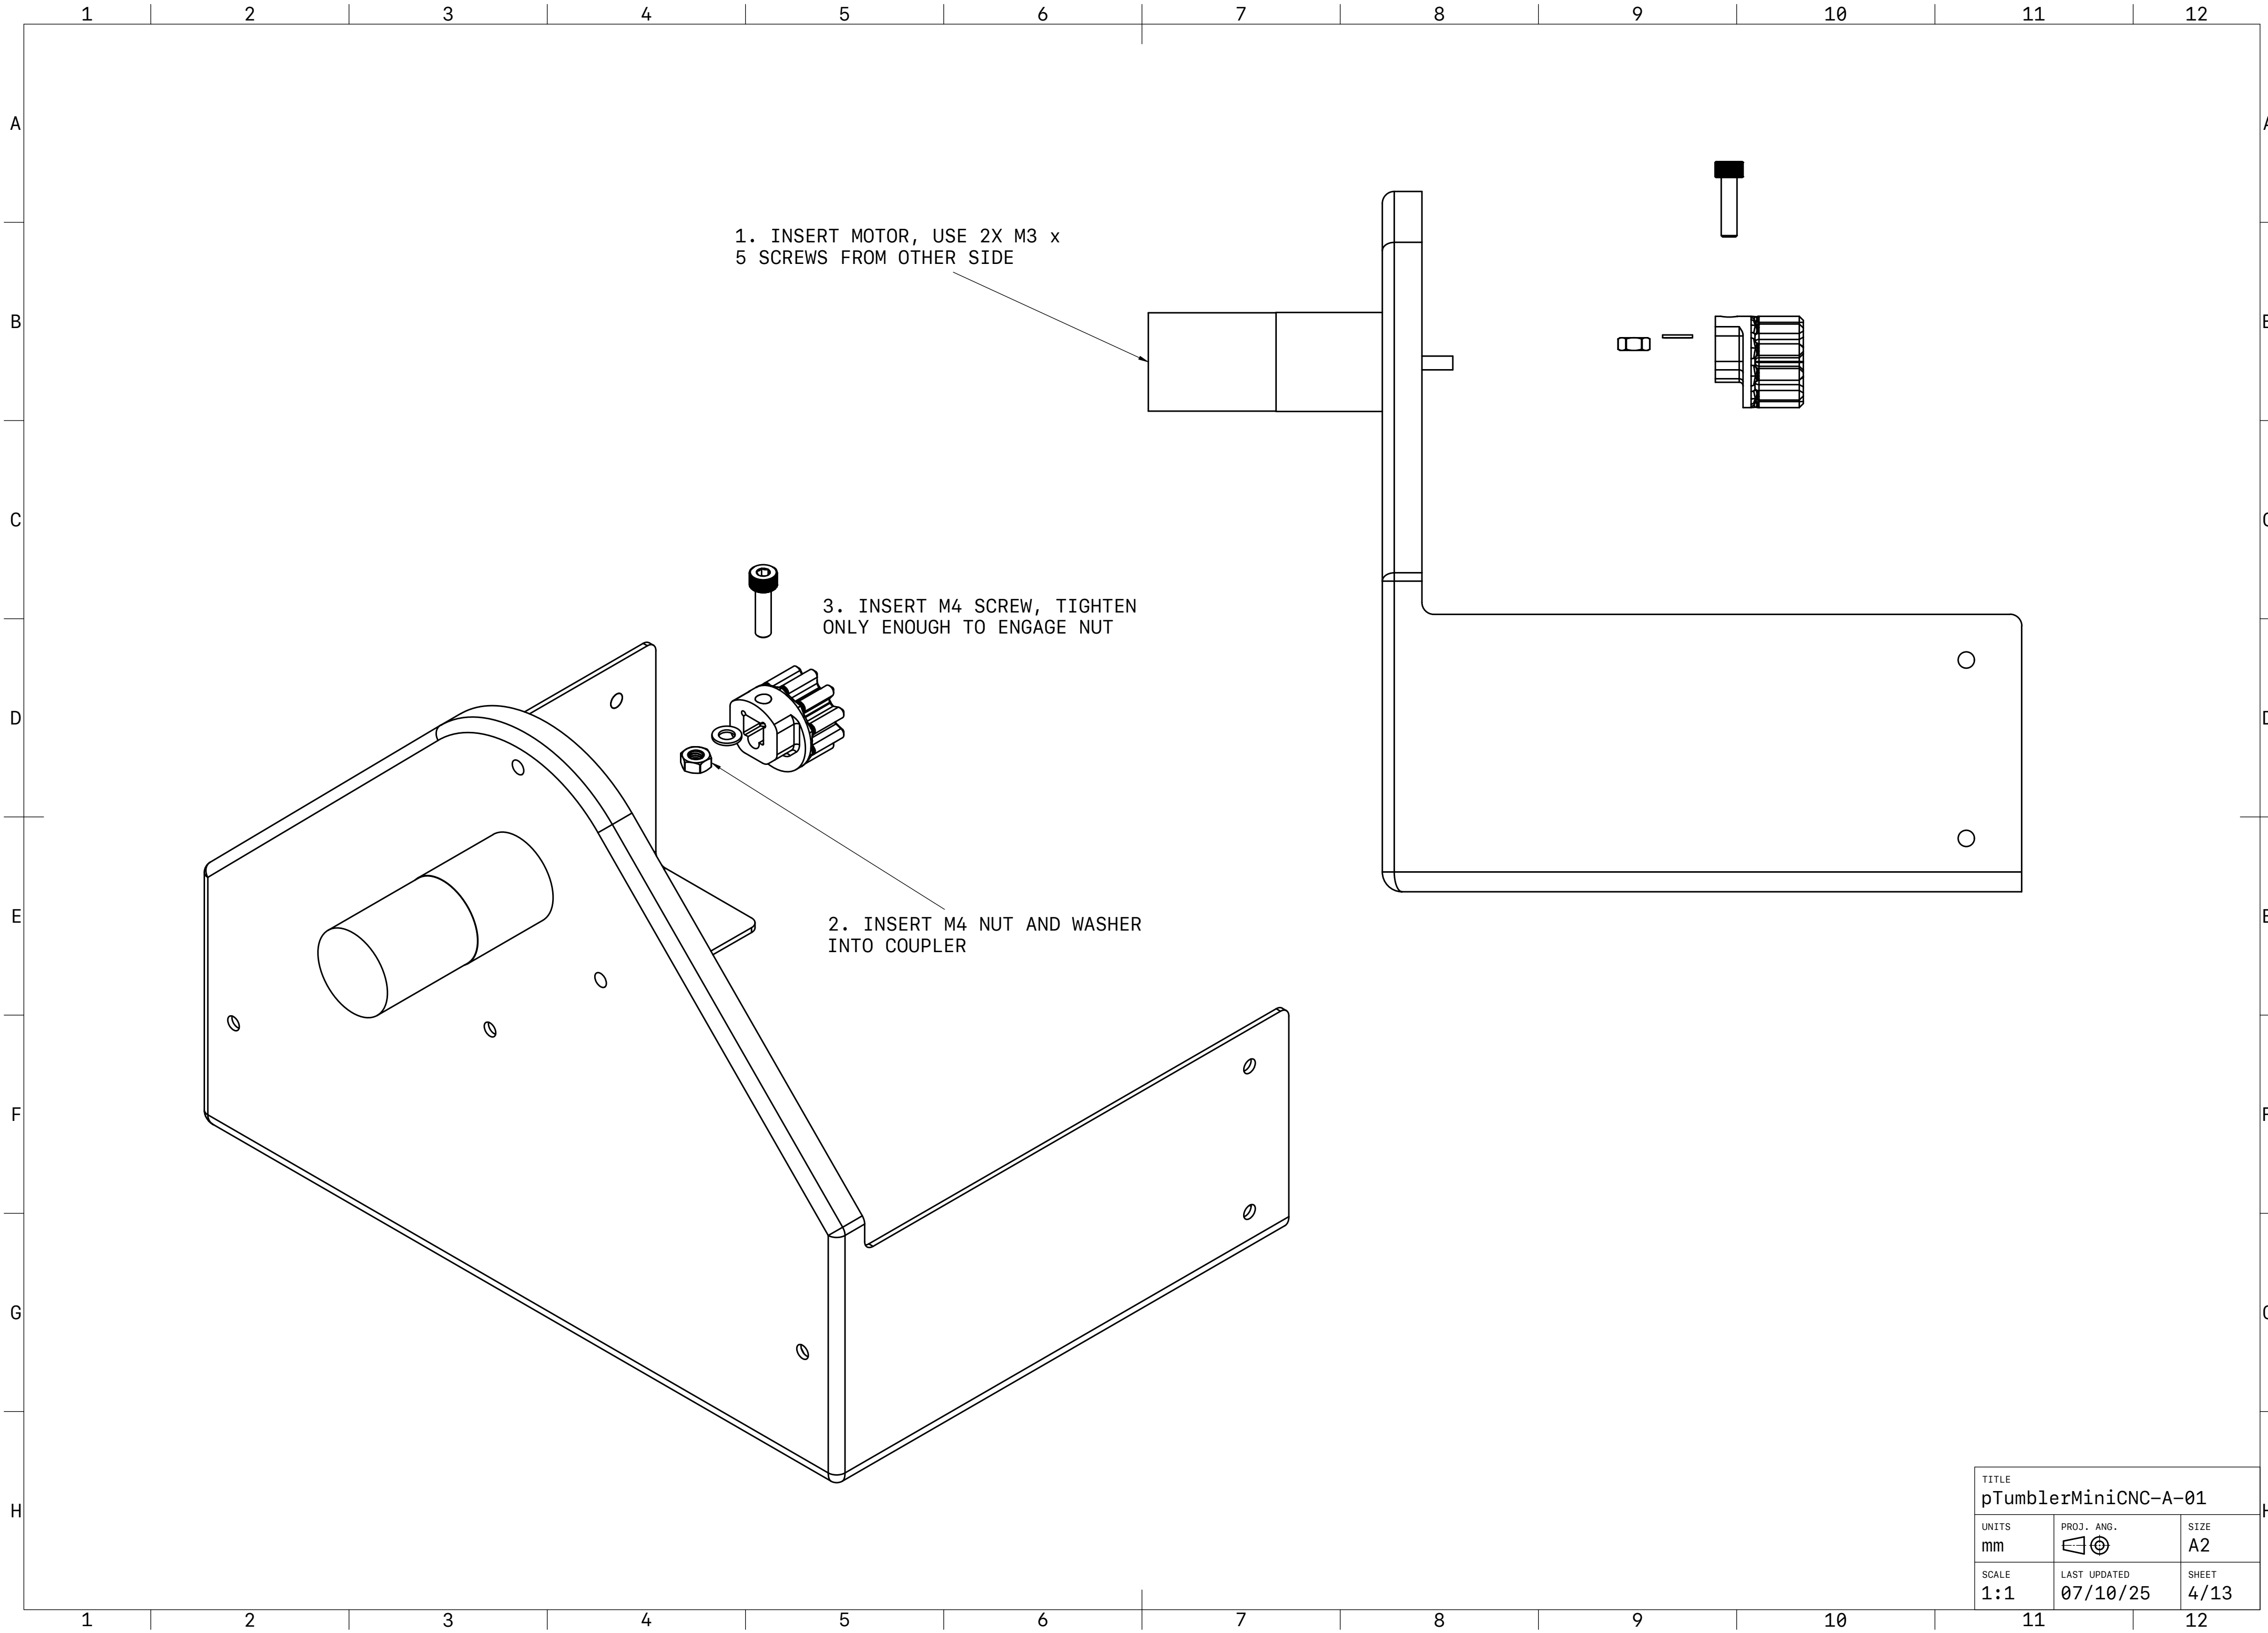

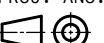TITLE pTumblerMiniCNC-A-01		
UNITS mm	PROJ. ANG. 	SIZE A2
SCALE 1:1	LAST UPDATED 07/10/25	SHEET 4/13

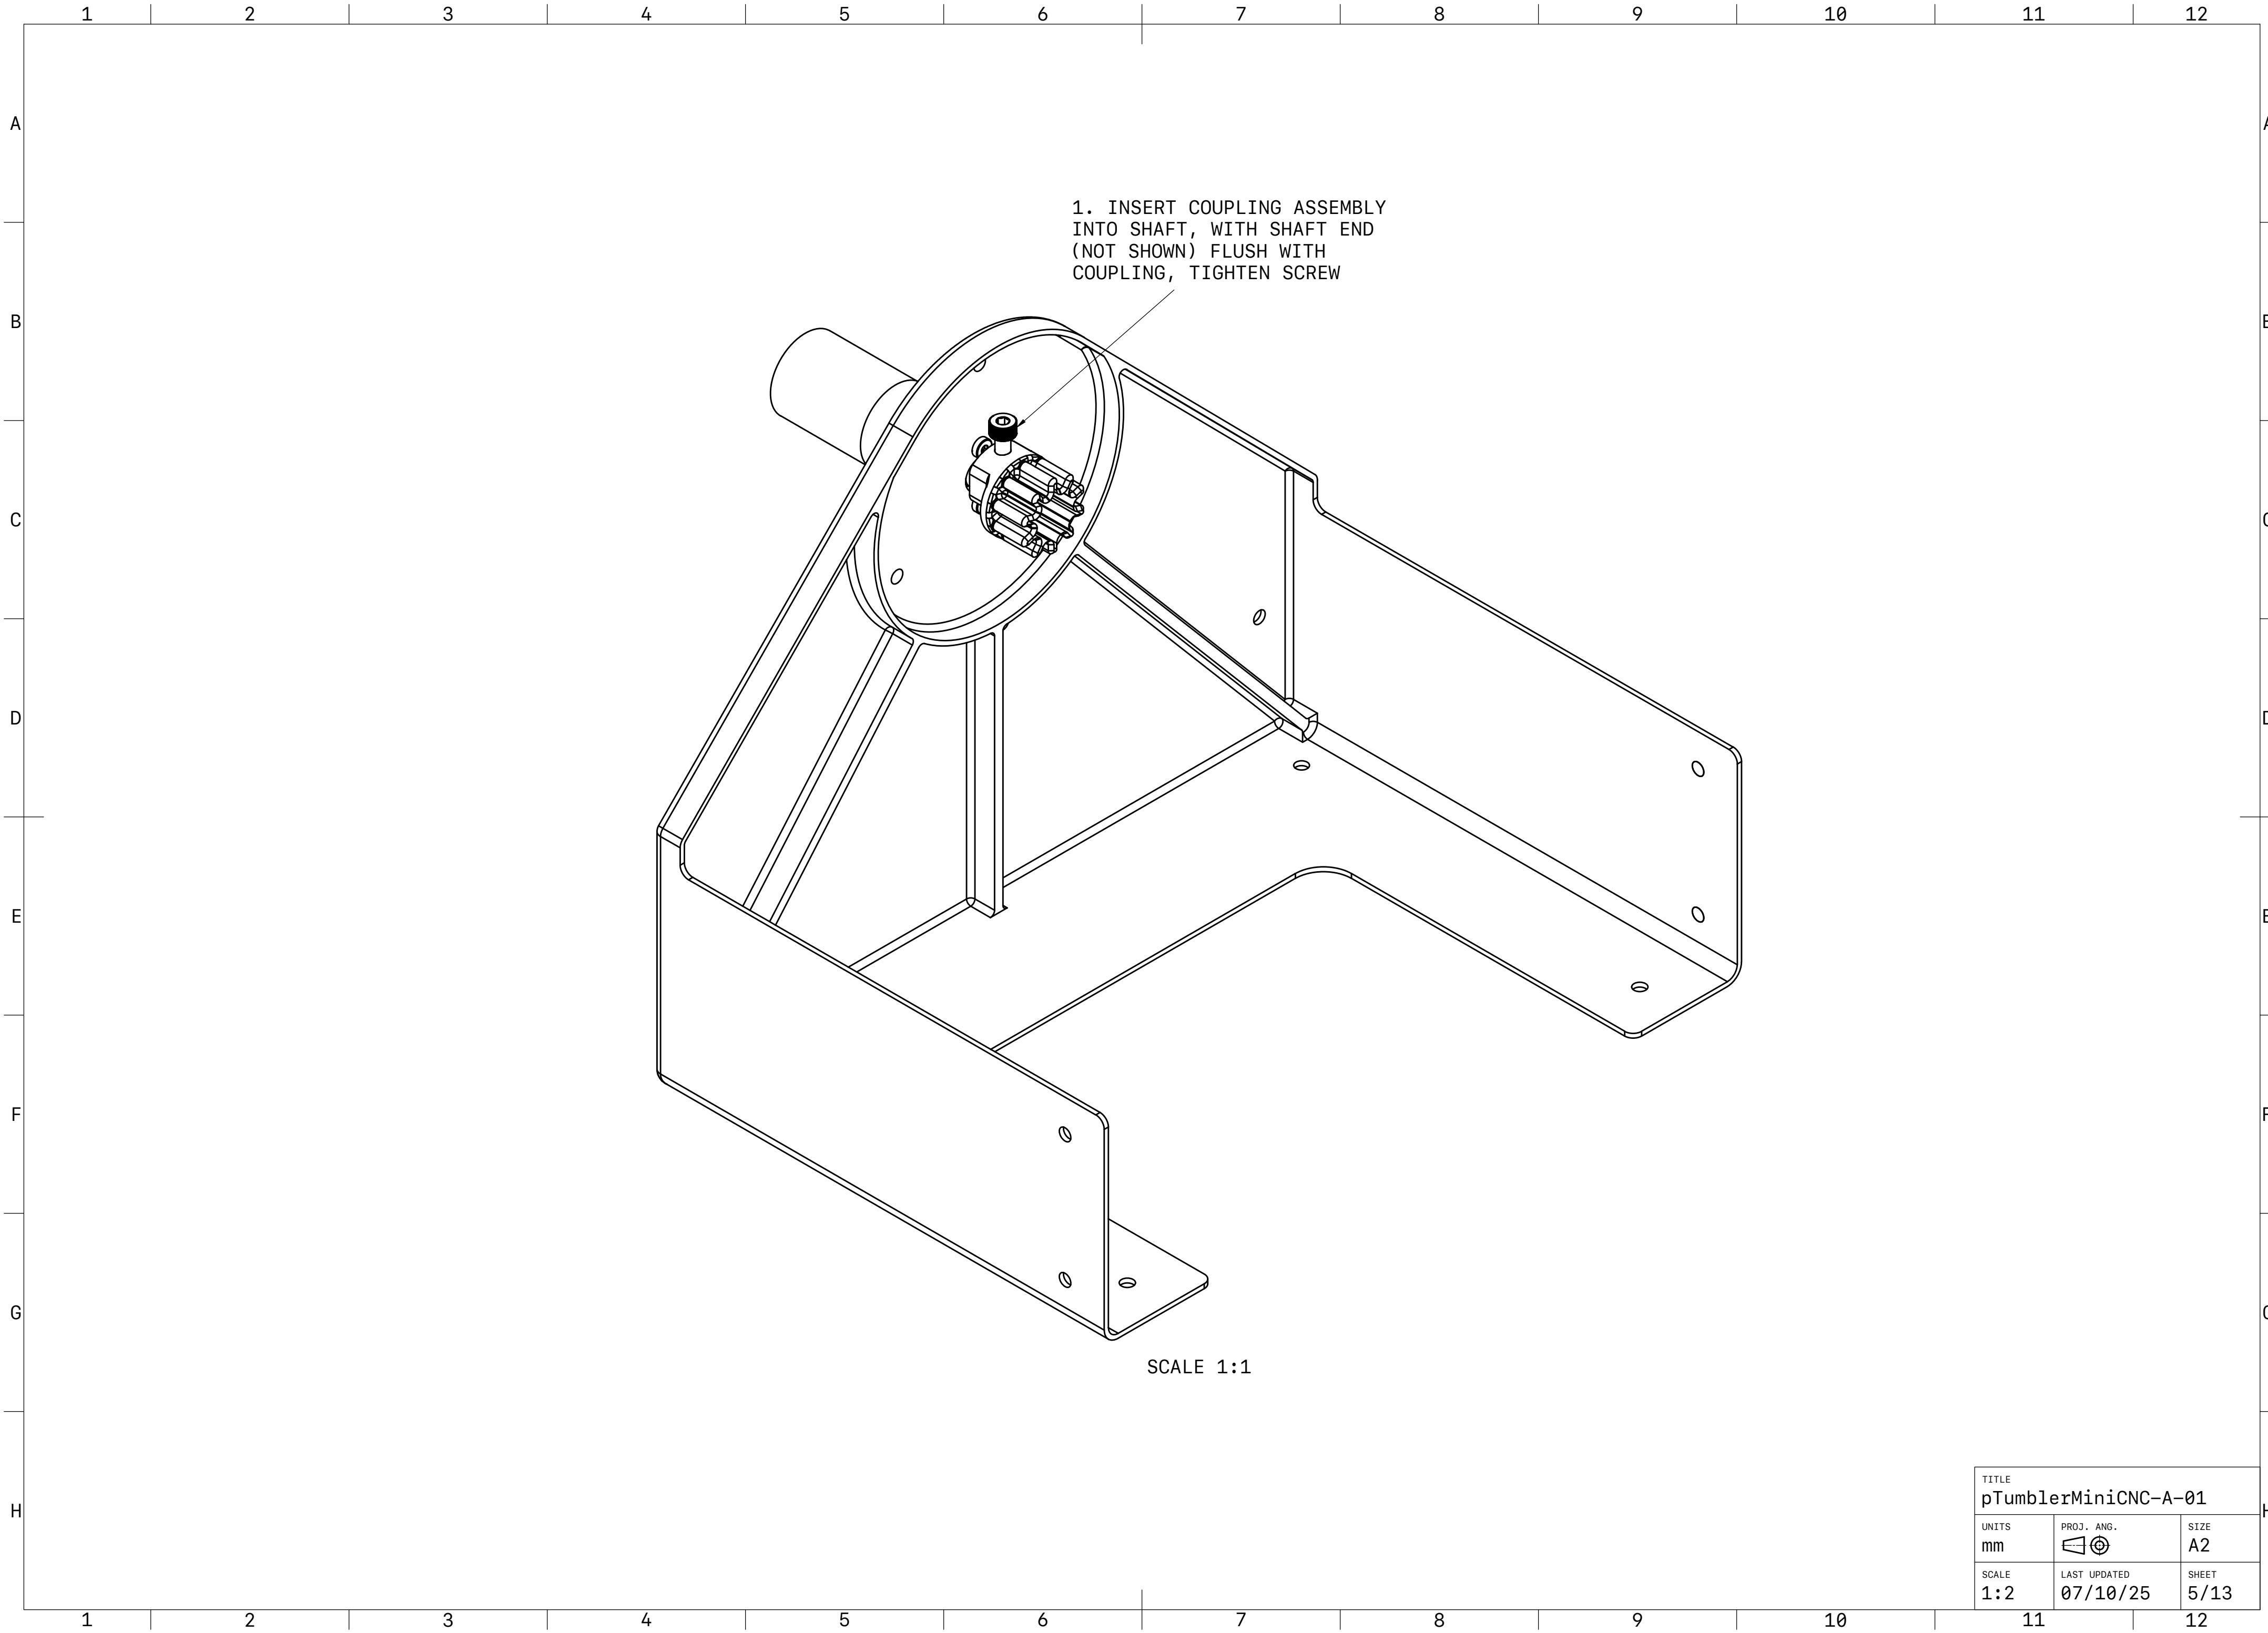

TITLE pTumblerMiniCNC-A-01		
UNITS mm	PROJ. ANG. 	SIZE A2
SCALE 1:2	LAST UPDATED 07/10/25	SHEET 5/13

12111097654321

BEARING 2 CARTRIDGE ASSEMBLY

A

B

C

D

E

F

G

H

A

B

C


D

E

F

G

H

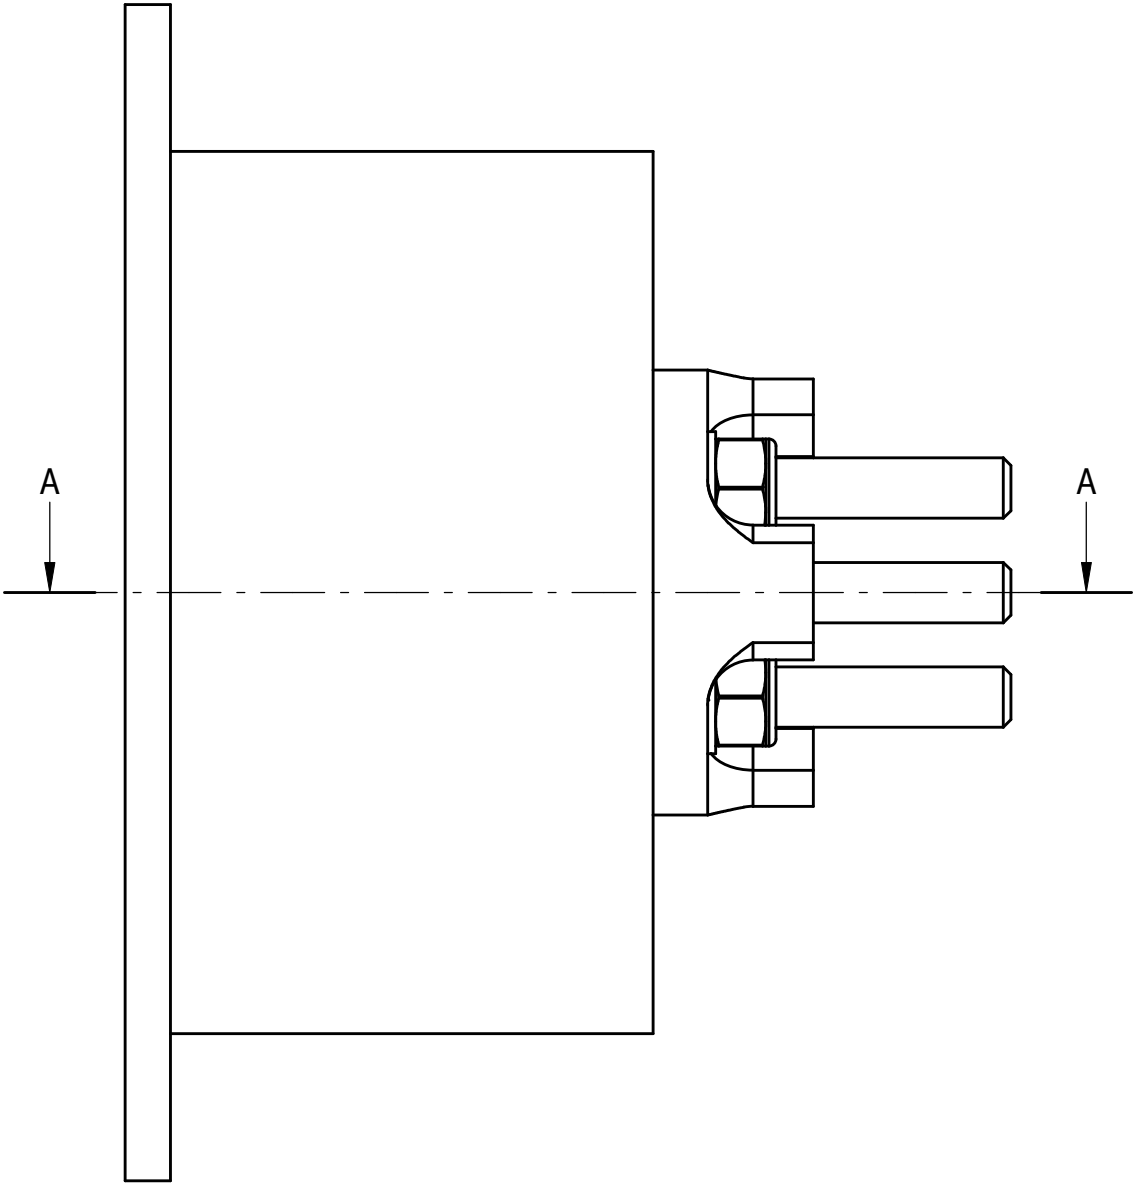


SCALE 2:1

1. INSERT INNER BEARING SLEEVE

2. INSERT 3X M4 X 40 SCREWS

3. TIGHTEN 3X NUTS

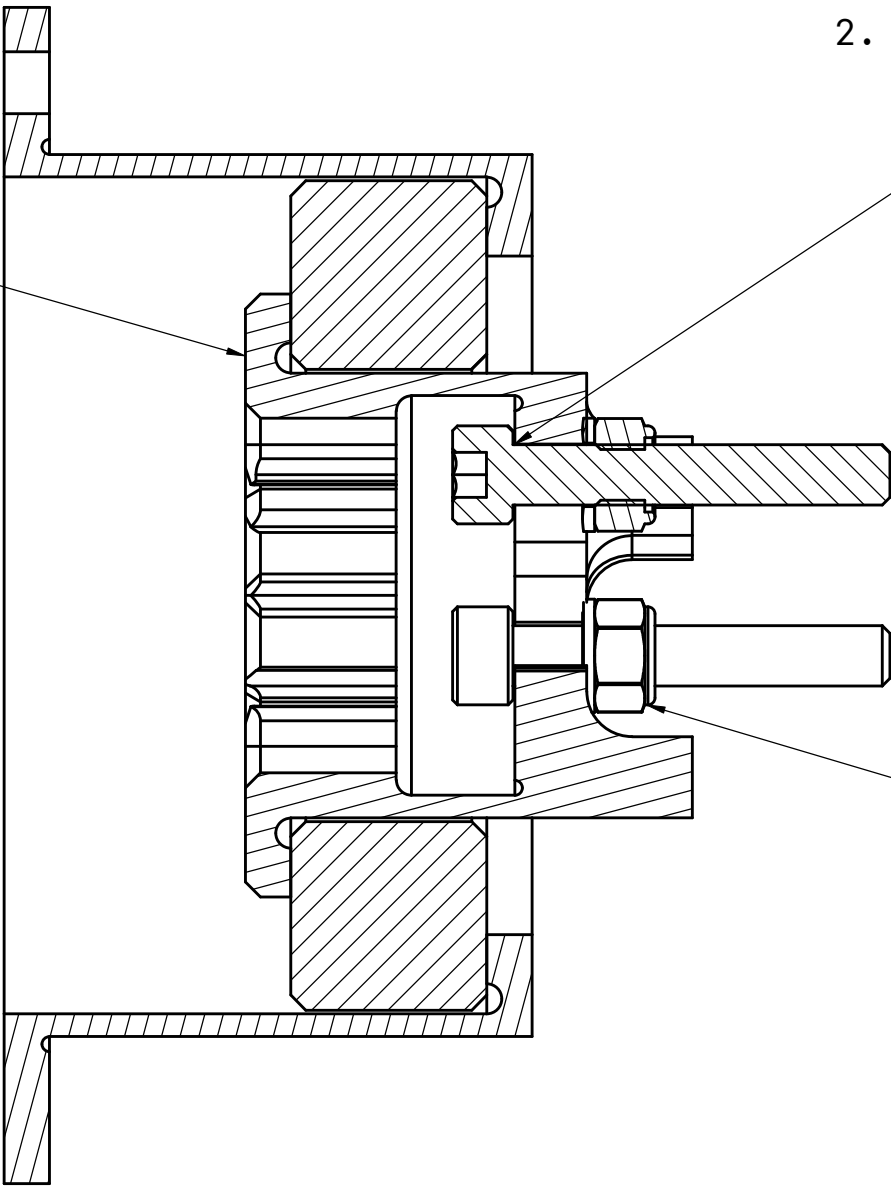

A-A
SCALE 2:1

TITLE pTumblerMiniCNC-A-01		
UNITS mm	PROJ. ANG. 	SIZE A2
SCALE 1:1	LAST UPDATED 07/10/25	SHEET 6/13

12111097654321

A
B
C
D
E
F
G
H

A
E
C
D
E
F
C
H

B

D

E

F

G

H

E


C

2

EF

C

	H
--	---

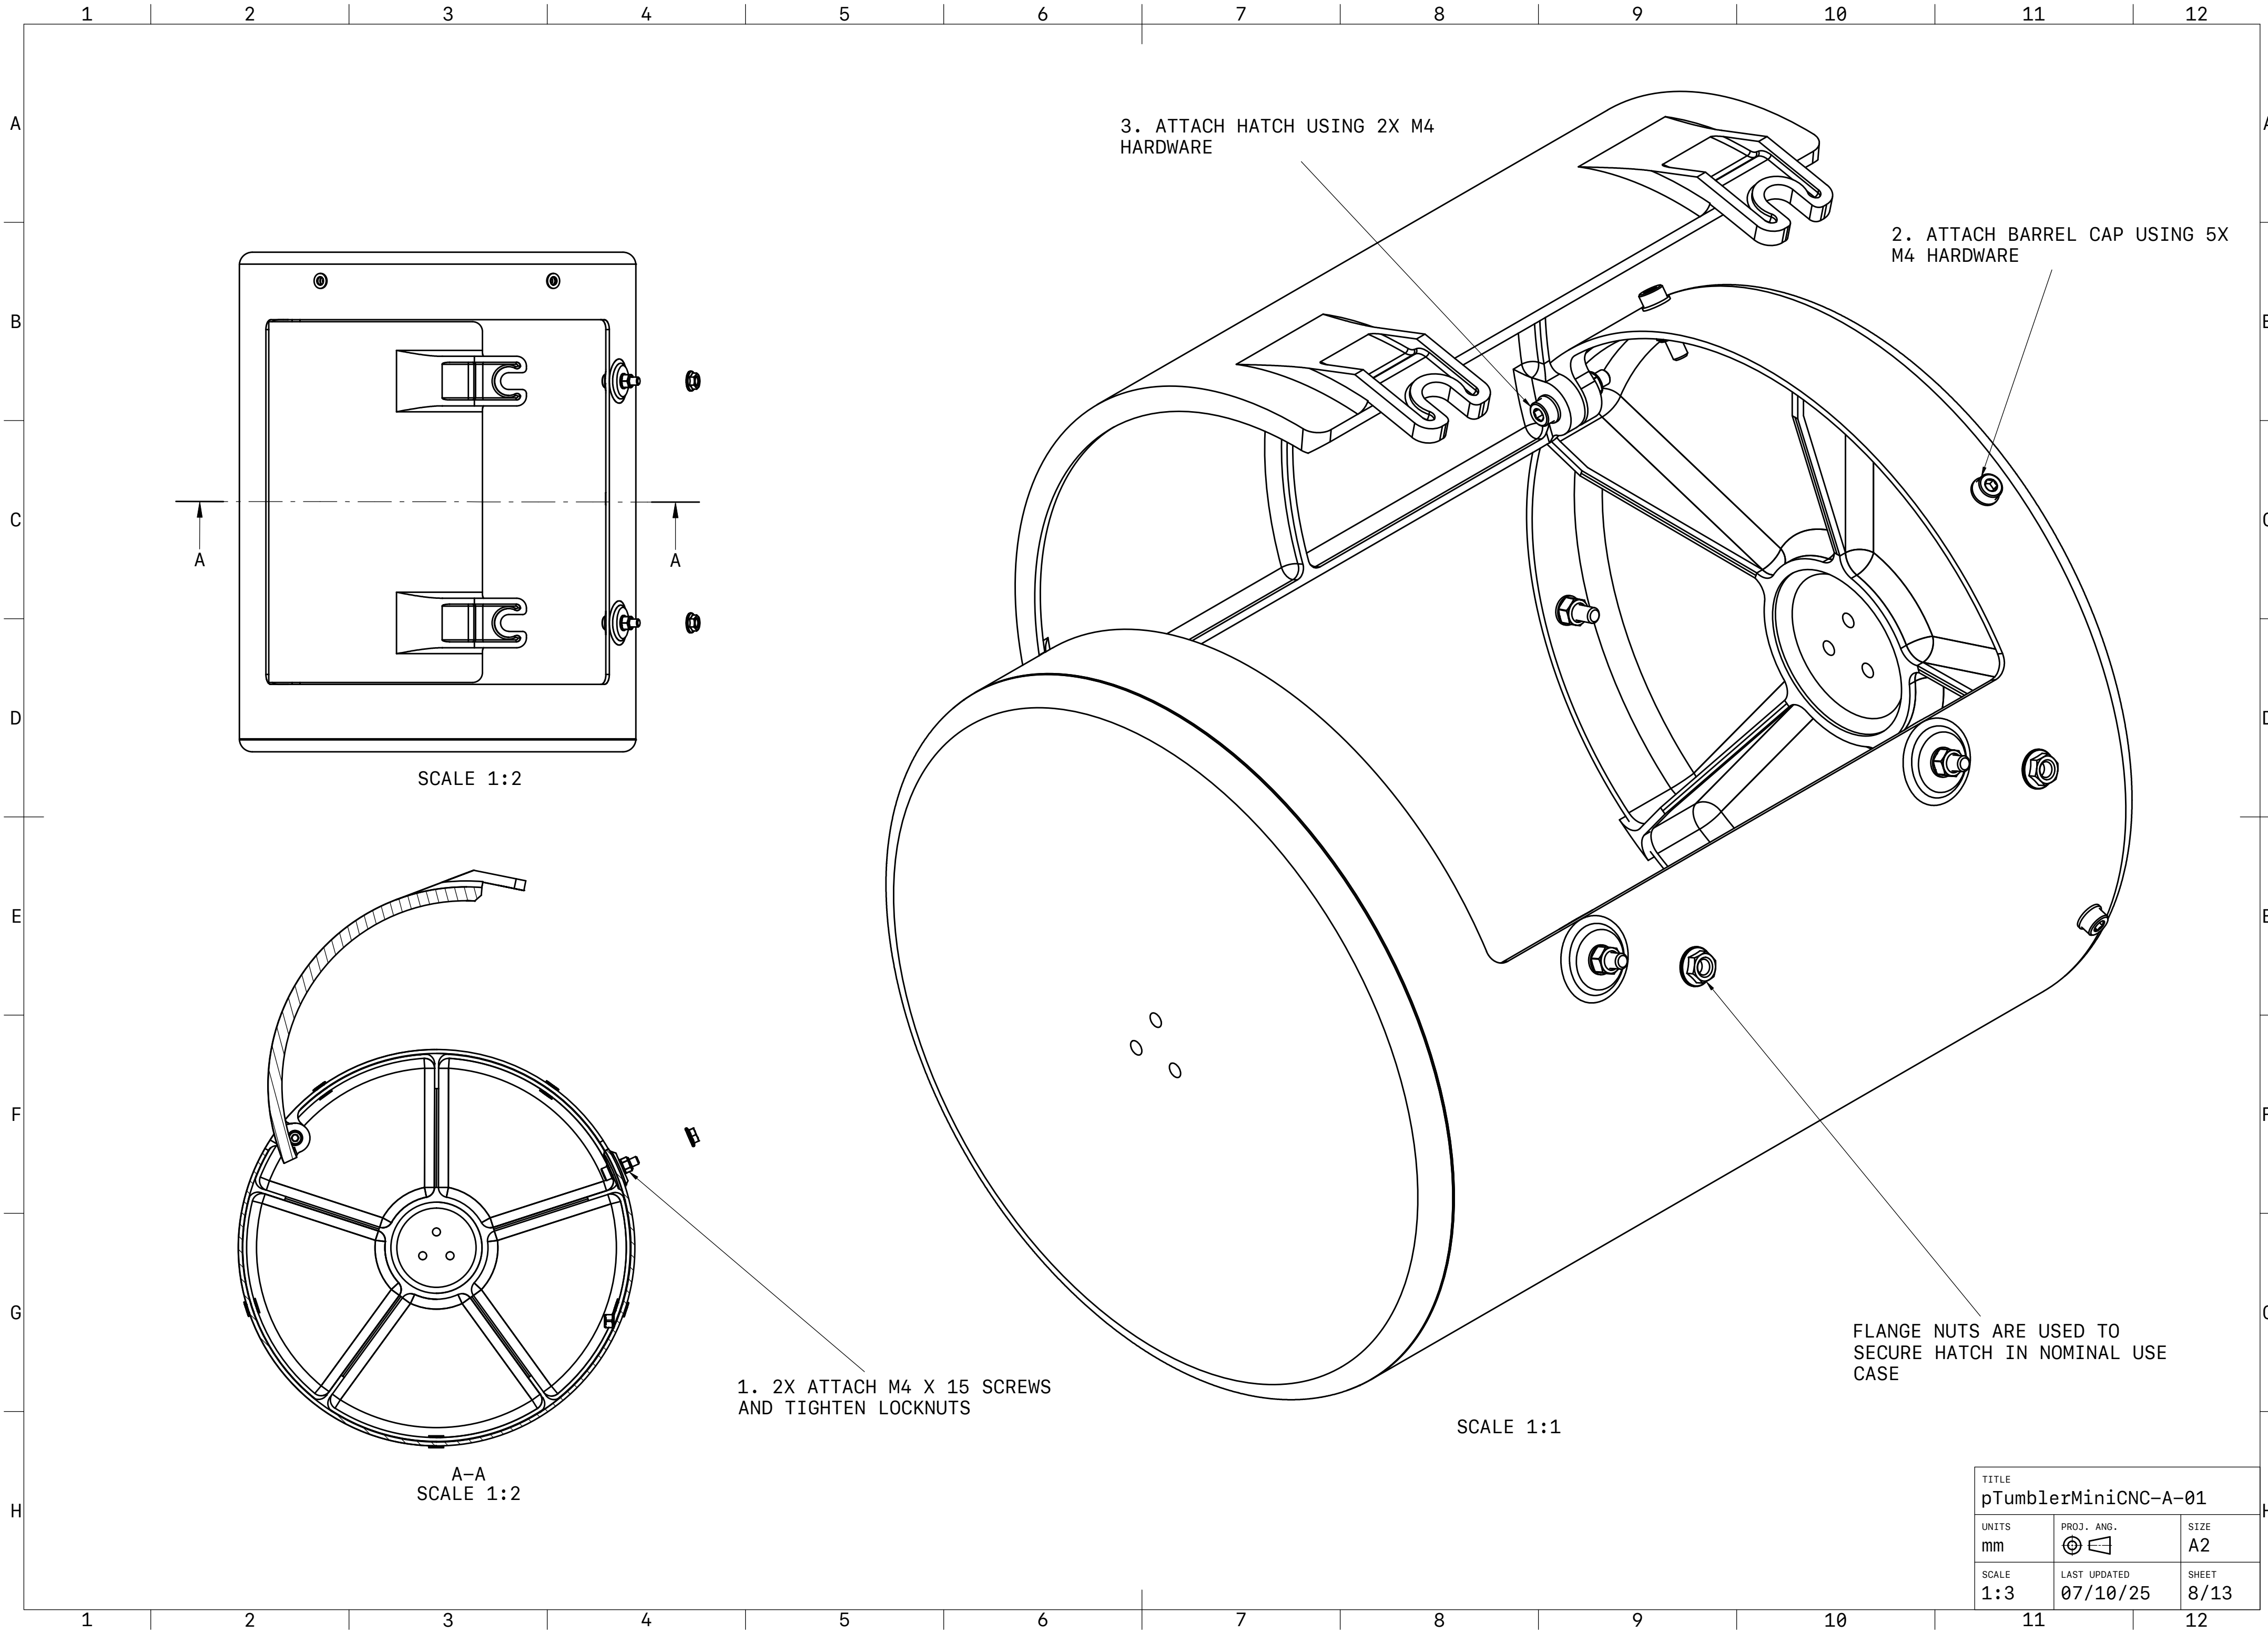

1. 2X ATTACH M4 X 15 SCREWS
AND TIGHTEN LOCKNUTS

3. ATTACH HATCH USING 2X M4
HARDWARE

2. ATTACH BARREL CAP USING 5X
M4 HARDWARE


FLANGE NUTS ARE USED TO
SECURE HATCH IN NOMINAL USE
CASE

SCALE 1:2

A-A
SCALE 1:2

SCALE 1:1

TITLE pTumblerMiniCNC-A-01		
UNITS mm	PROJ. ANG. 	SIZE A2
SCALE 1:3	LAST UPDATED 07/10/25	SHEET 8/13

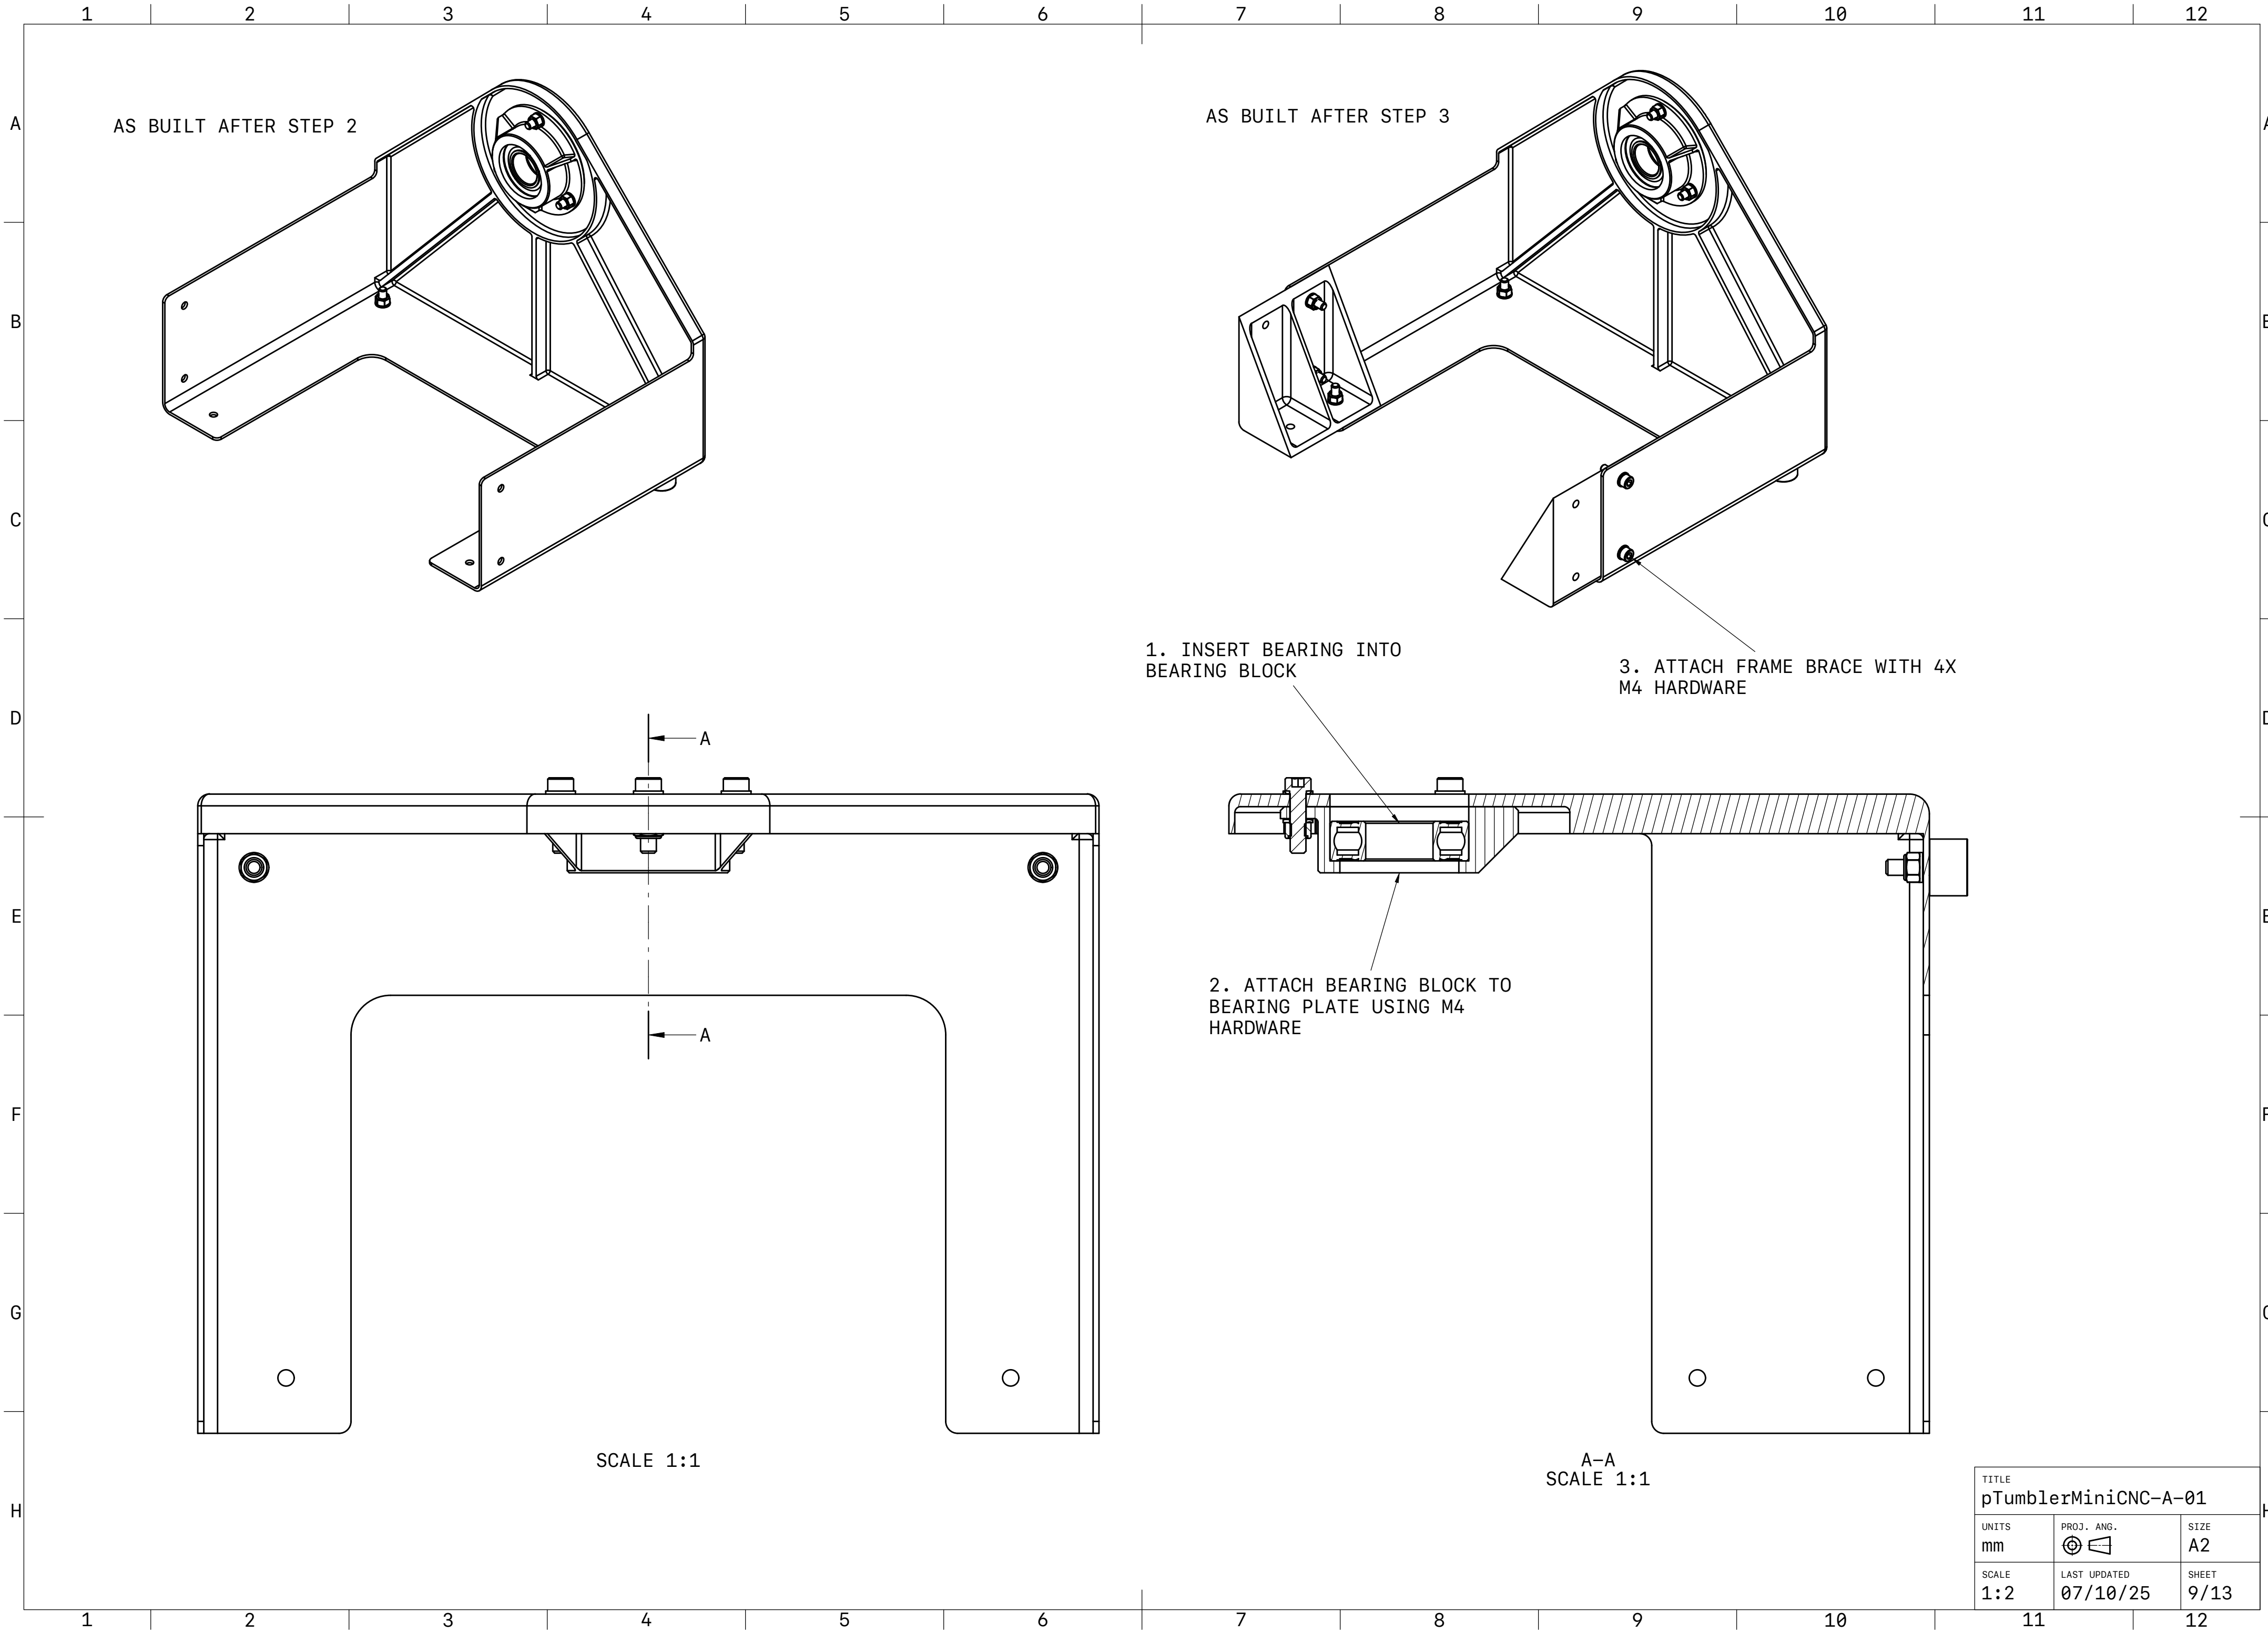

AS BUILT AFTER STEP 2

AS BUILT AFTER STEP 3

1. INSERT BEARING INTO BEARING BLOCK


3. ATTACH FRAME BRACE WITH 4X M4 HARDWARE


2. ATTACH BEARING BLOCK TO BEARING PLATE USING M4 HARDWARE

SCALE 1:1

A-A
SCALE 1:1

TITLE pTumblerMiniCNC-A-01		
UNITS mm	PROJ. ANG. ⊕	SIZE A2
SCALE 1:2	LAST UPDATED 07/10/25	SHEET 9/13

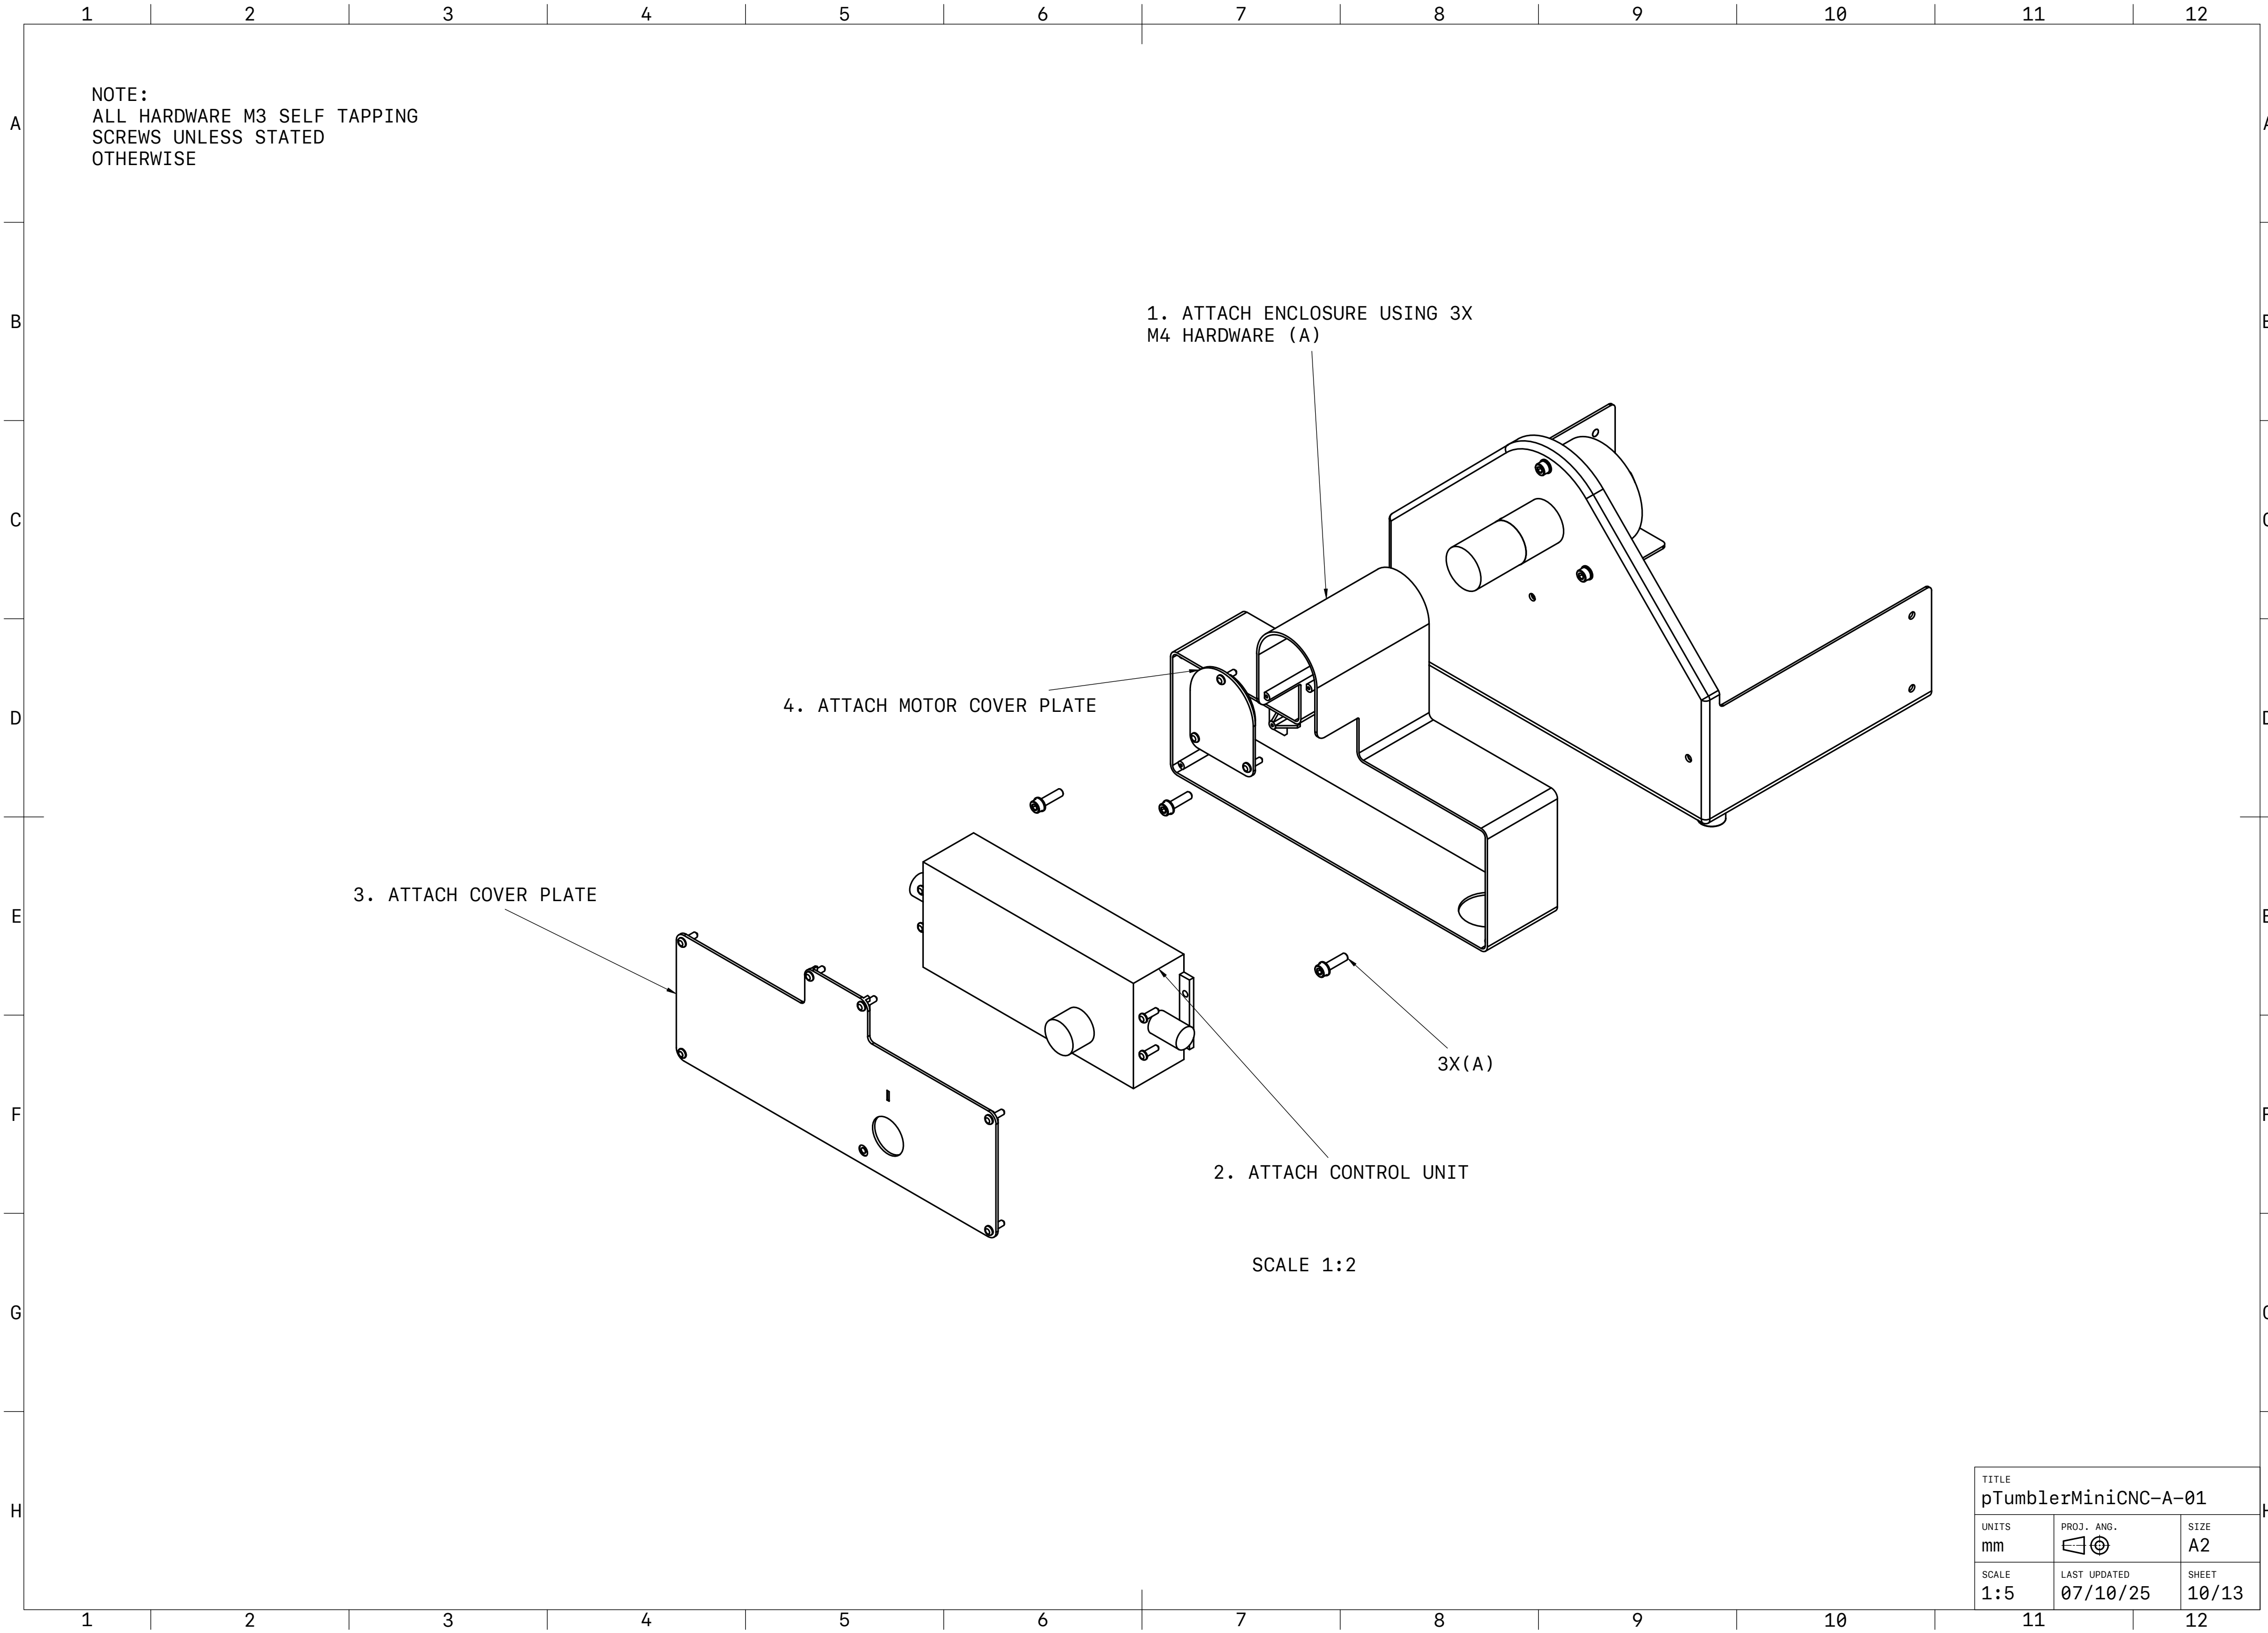


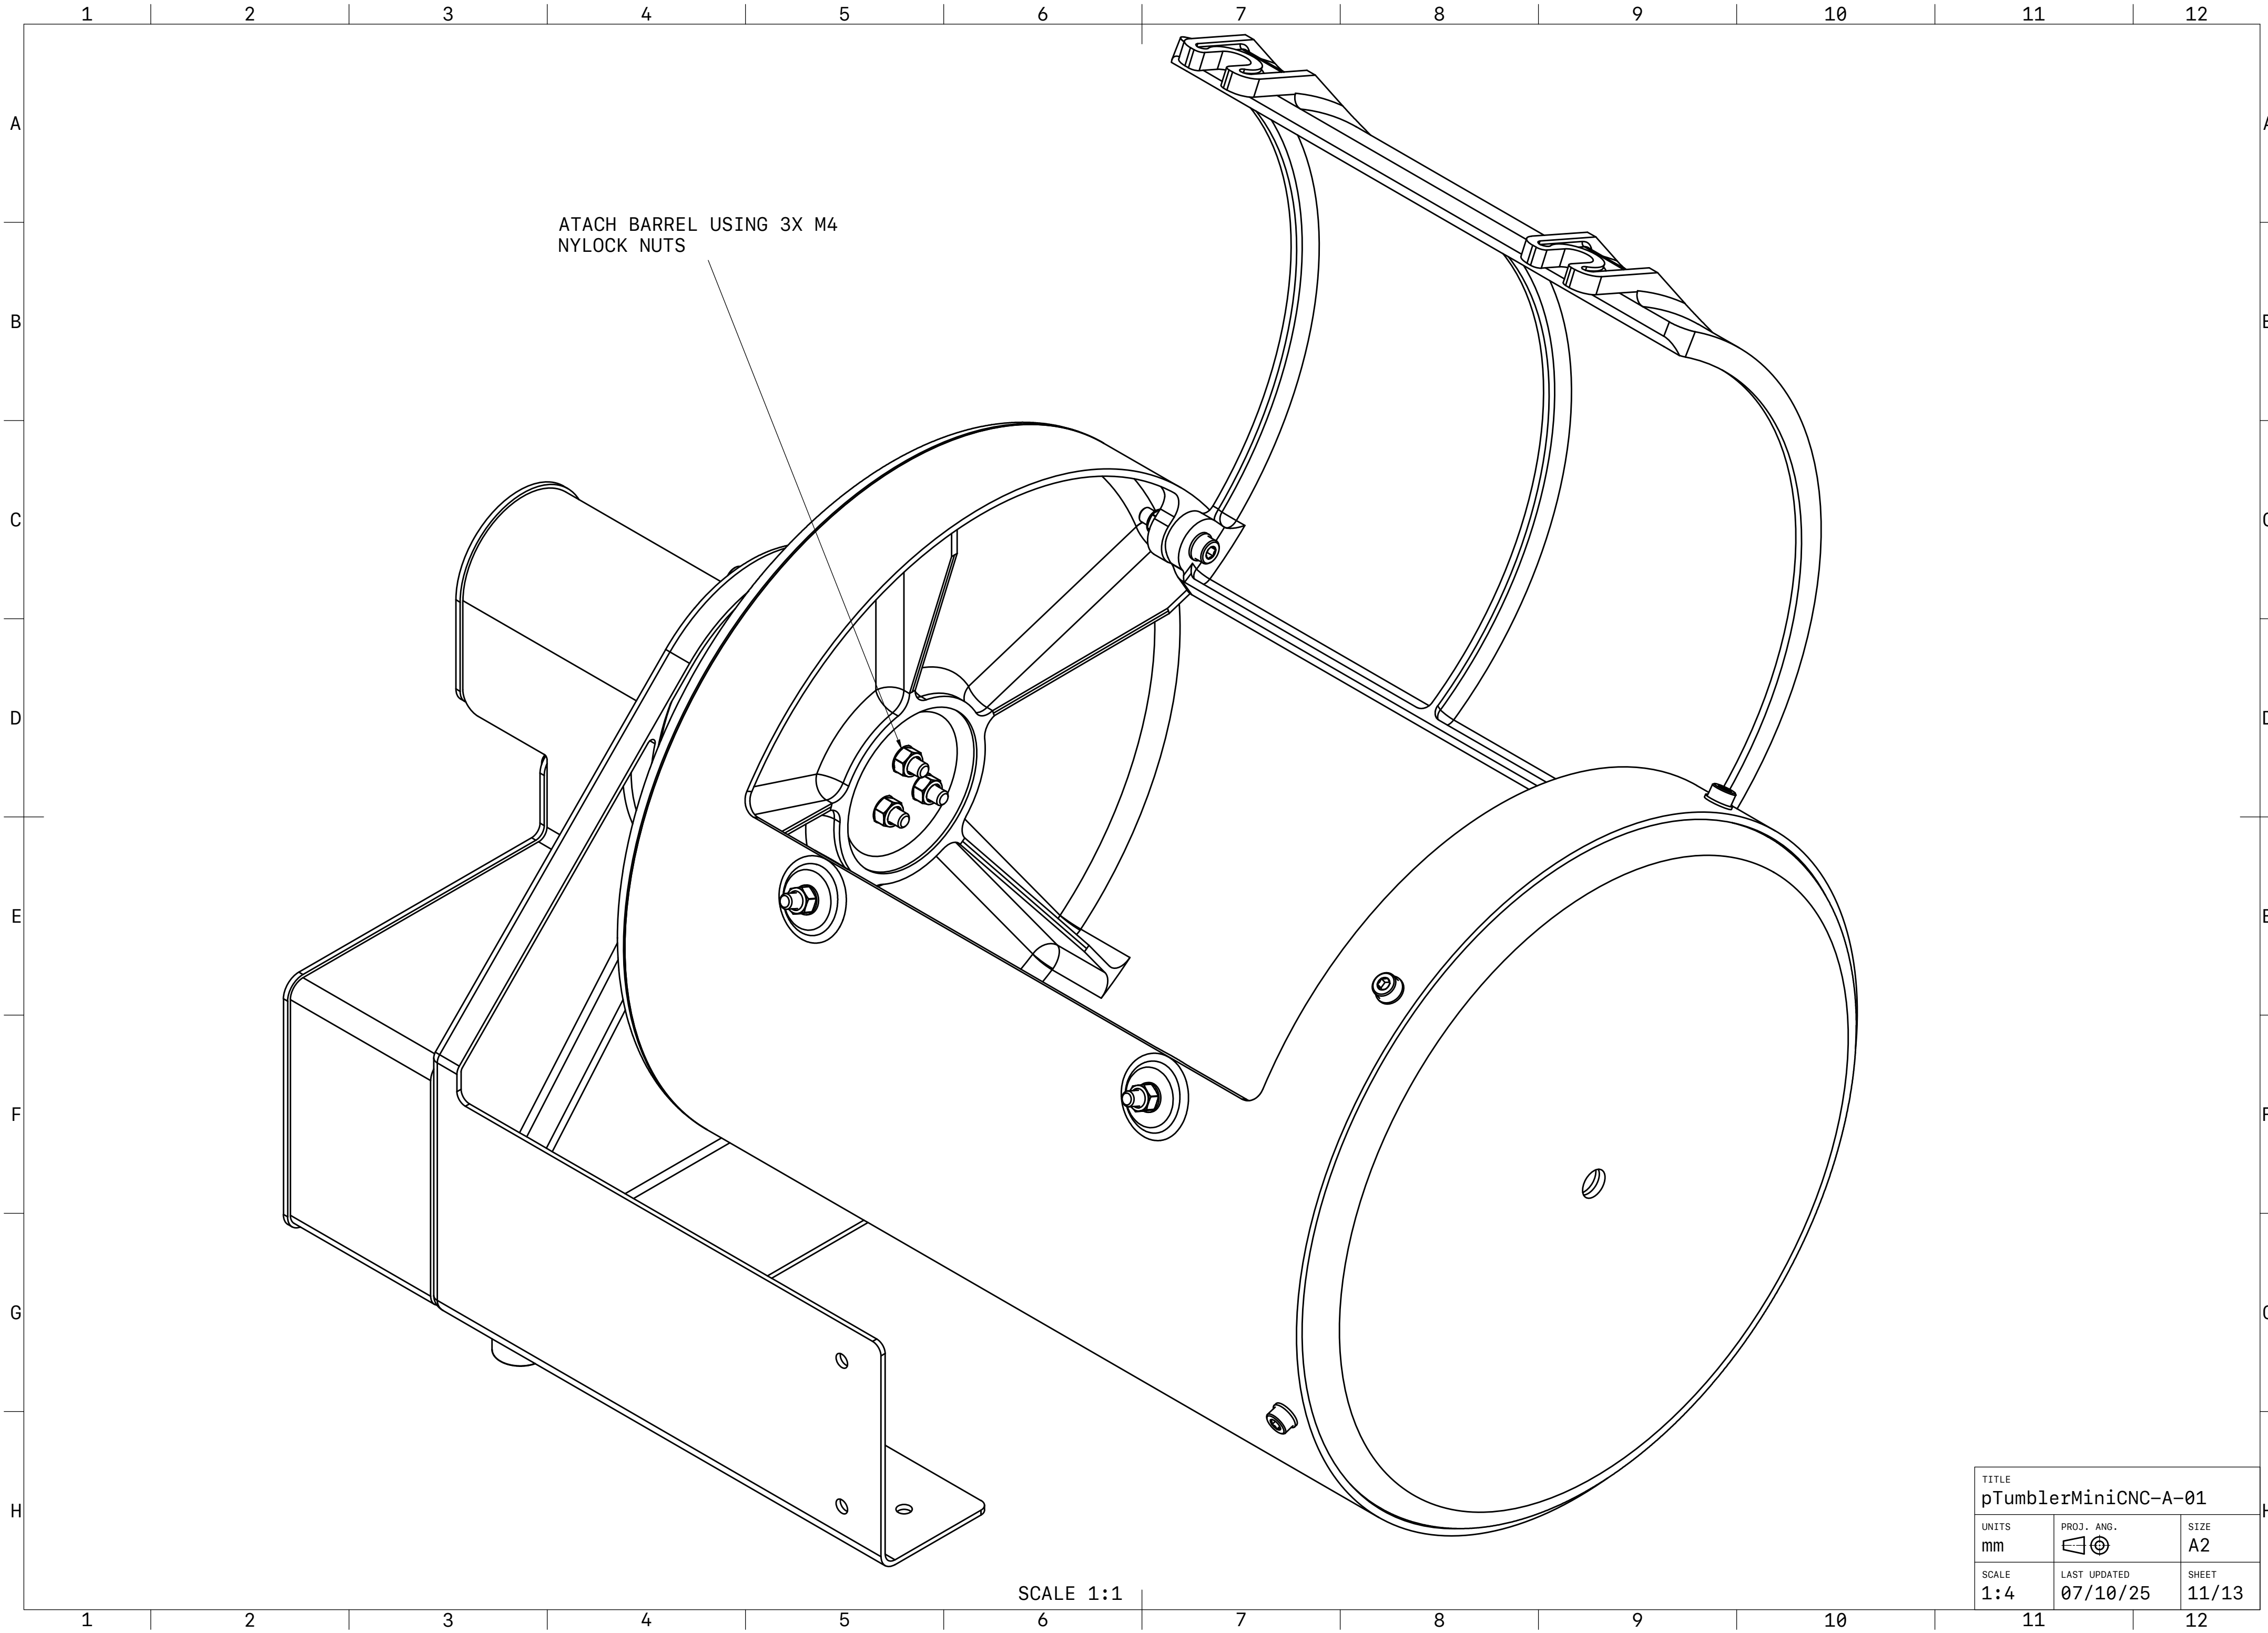

ATCH BARREL USING 3X M4
NYLOCK NUTS

SCALE 1:1

TITLE pTumblerMiniCNC-A-01		
UNITS mm	PROJ. ANG. 	SIZE A2
SCALE 1:4	LAST UPDATED 07/10/25	SHEET 11/13

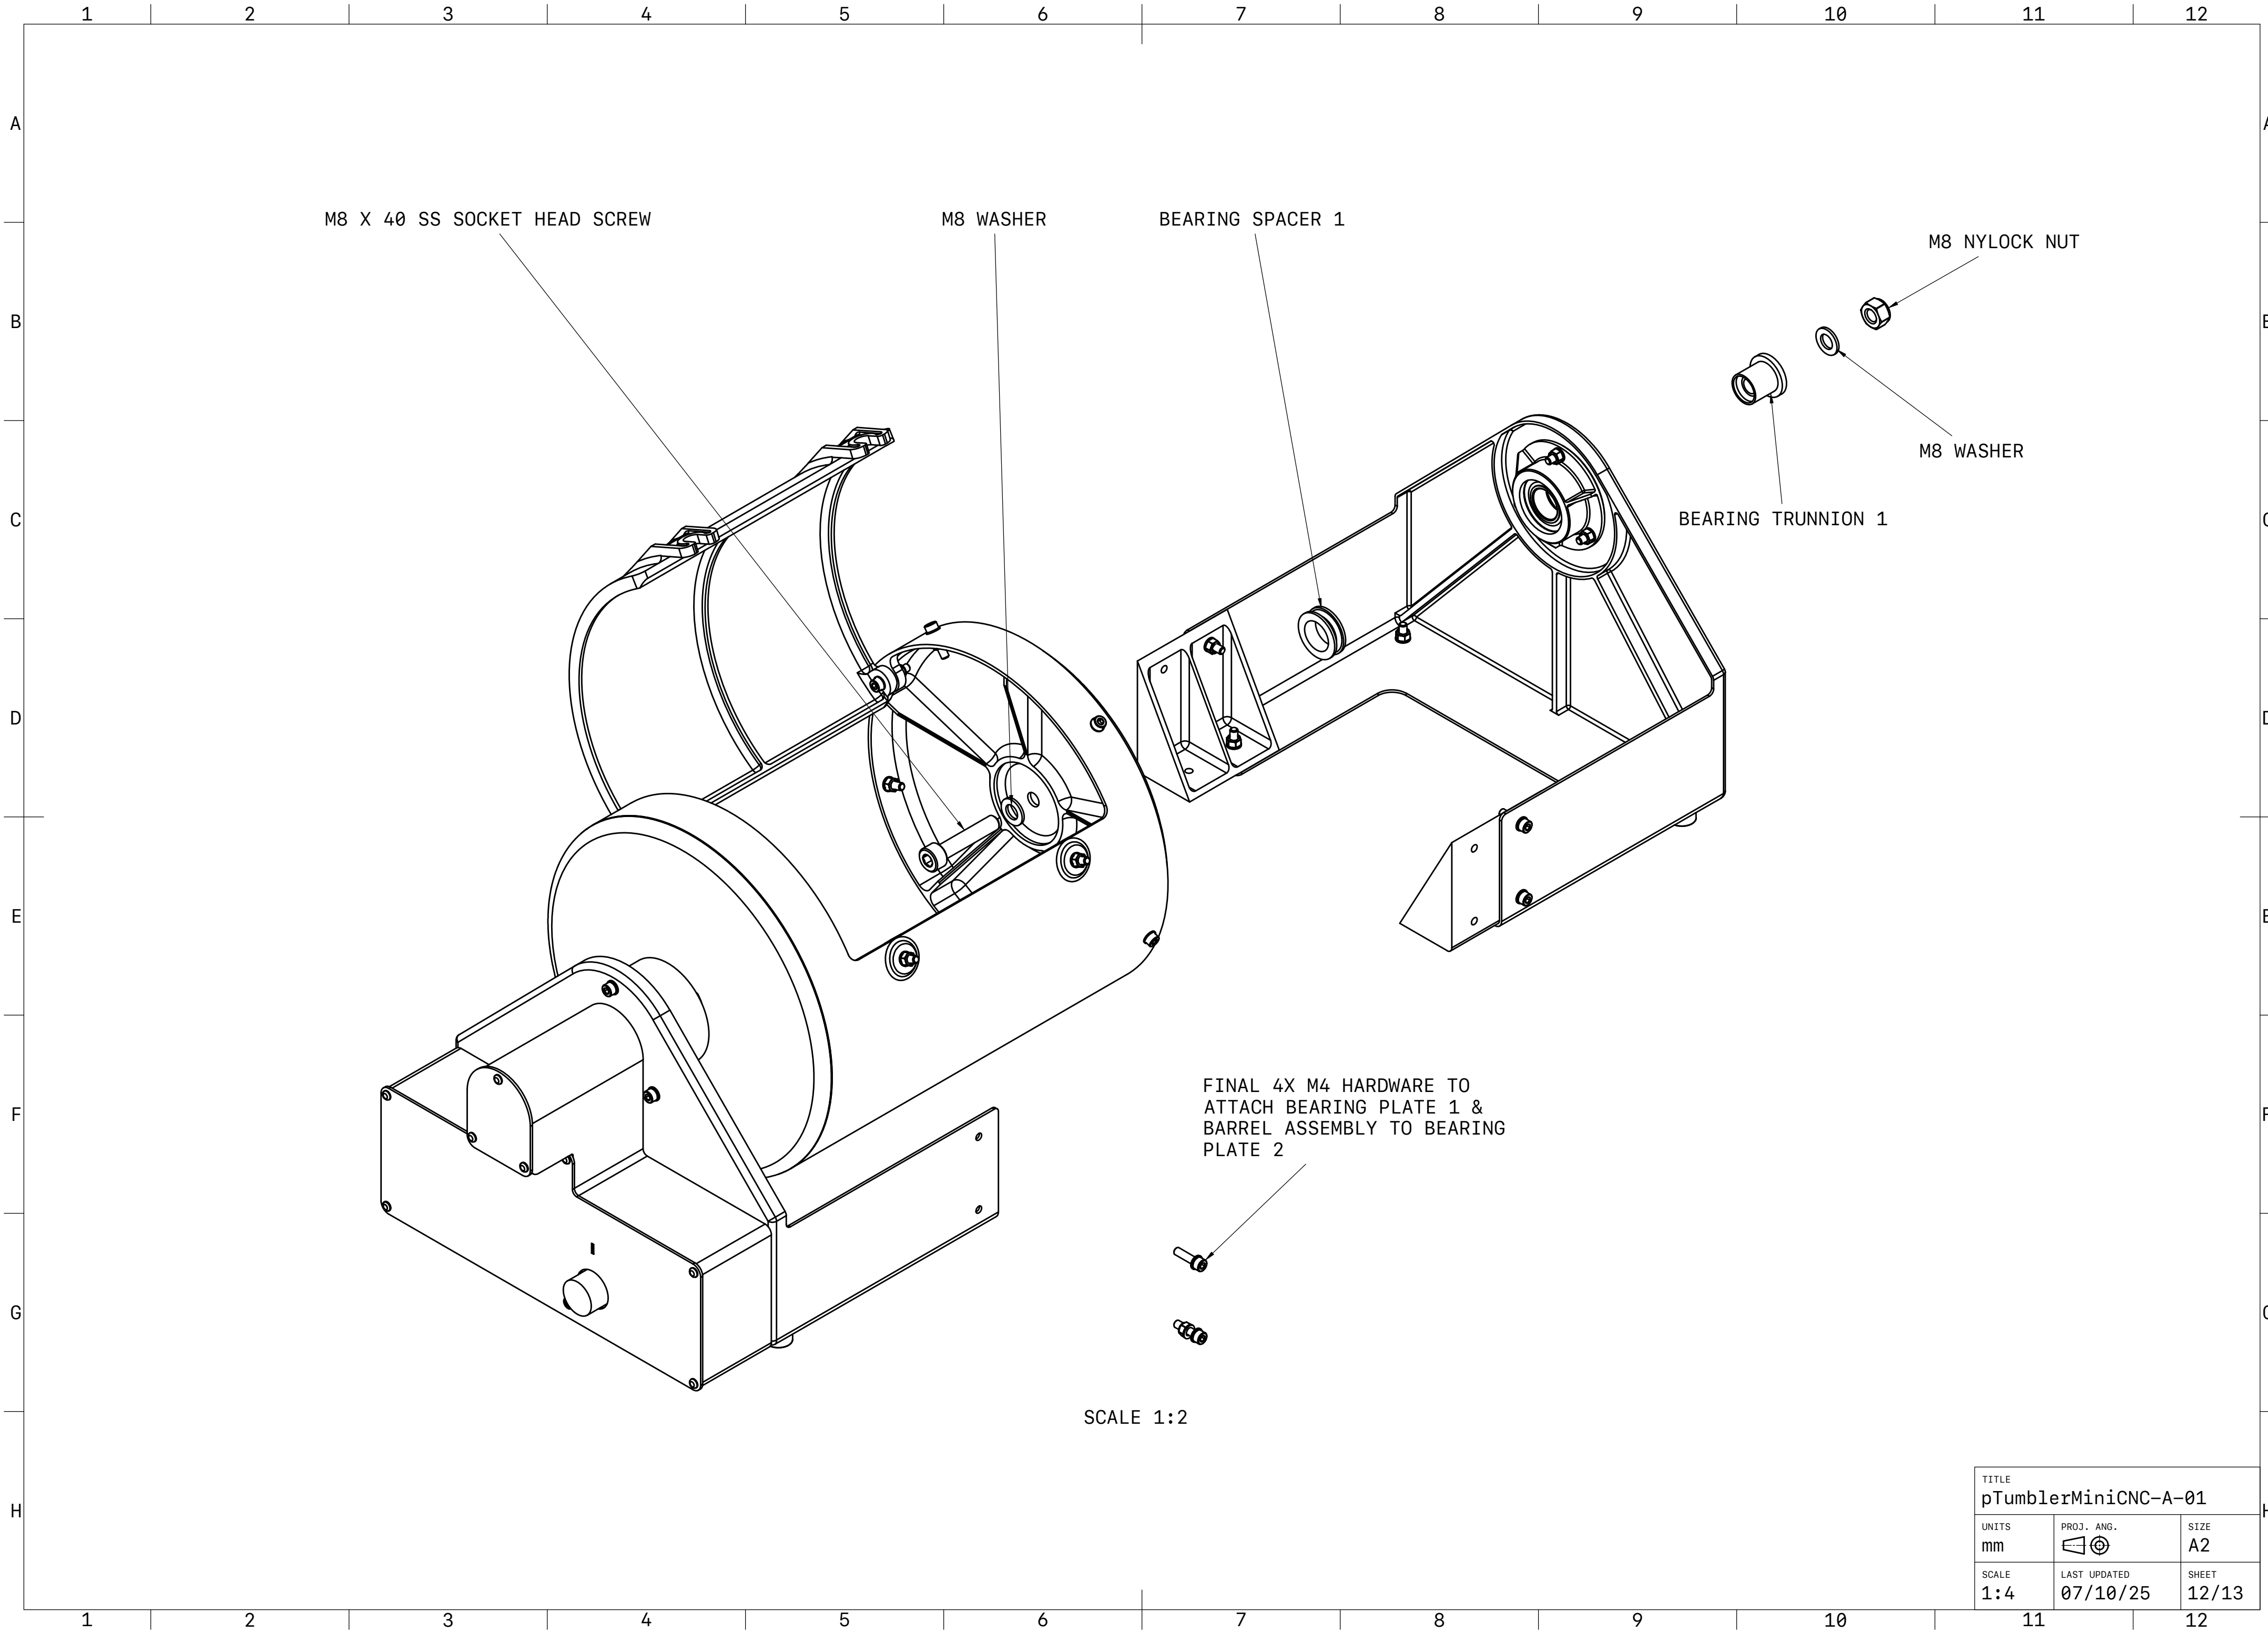

M8 X 40 SS SOCKET HEAD SCREW

M8 WASHER

BEARING SPACER 1

M8 NYLOCK NUT


M8 WASHER

BEARING TRUNNION 1

FINAL 4X M4 HARDWARE TO
ATTACH BEARING PLATE 1 &
BARREL ASSEMBLY TO BEARING
PLATE 2

SCALE 1:2

TITLE pTumblerMiniCNC-A-01		
UNITS mm	PROJ. ANG. 	SIZE A2
SCALE 1:4	LAST UPDATED 07/10/25	SHEET 12/13

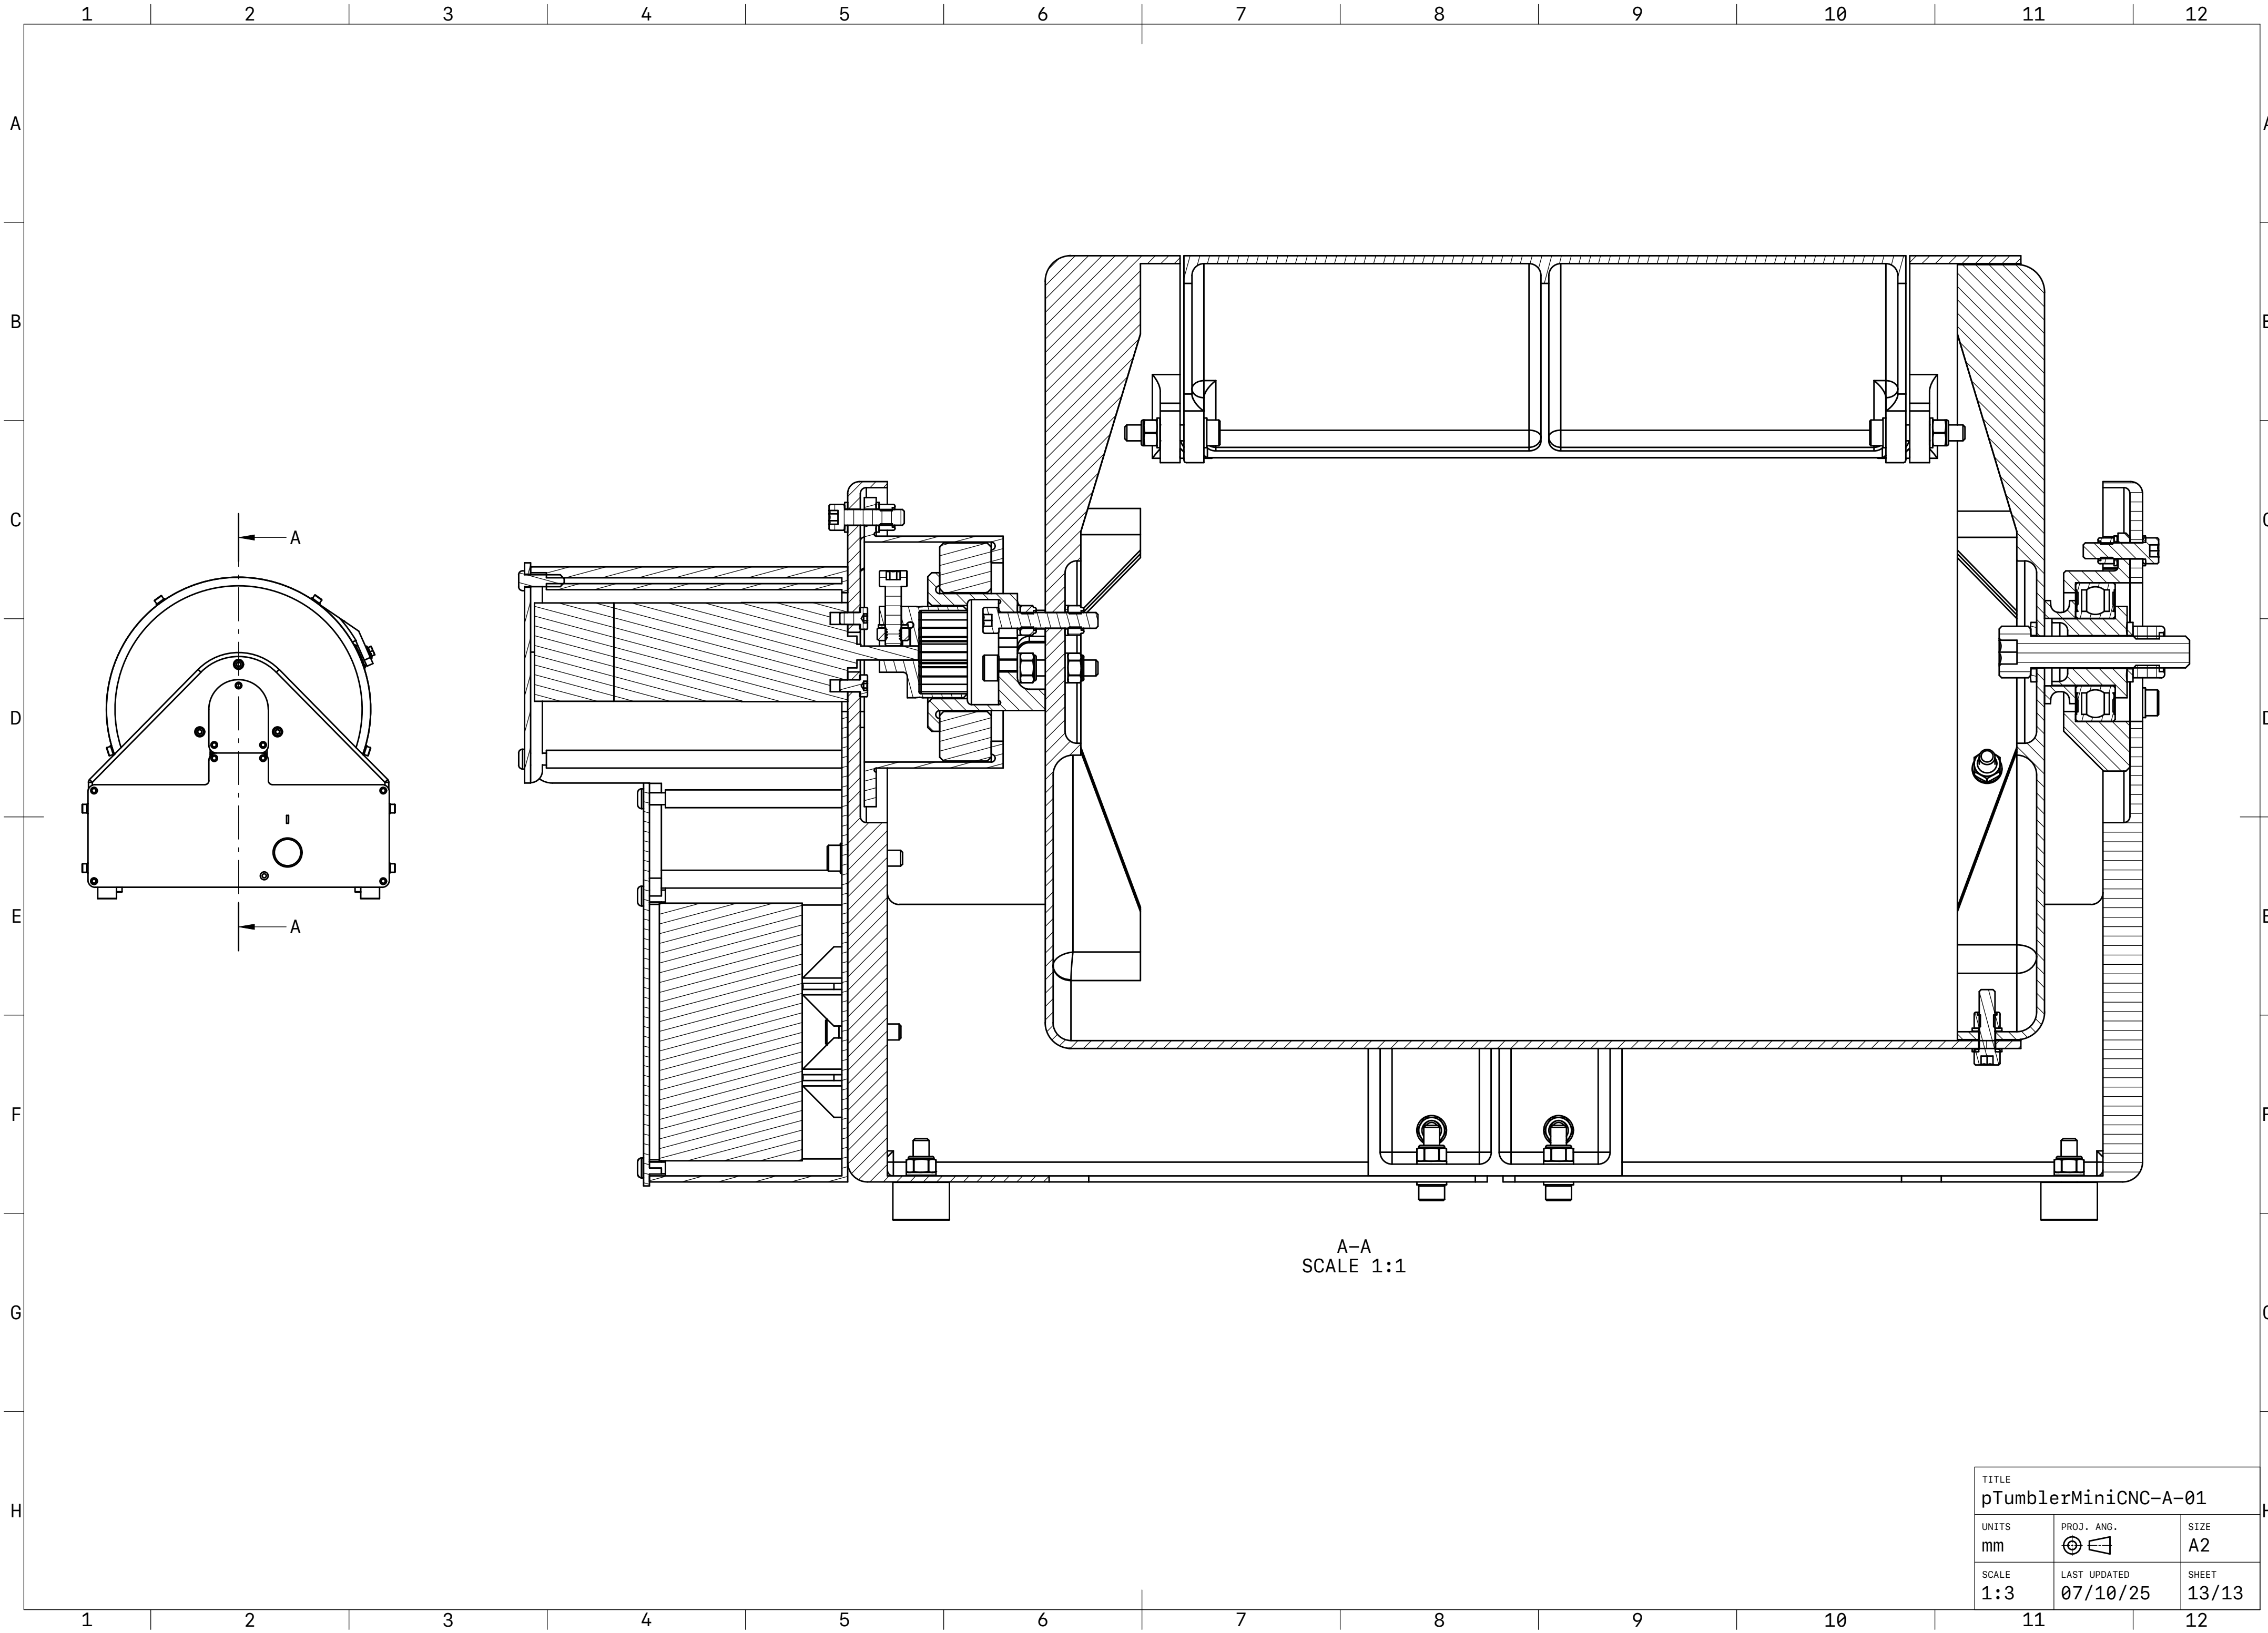

A-A
SCALE 1:1

TITLE pTumblerMiniCNC-A-01		
UNITS mm	PROJ. ANG. ⊕	SIZE A2
SCALE 1:3	LAST UPDATED 07/10/25	SHEET 13/13